
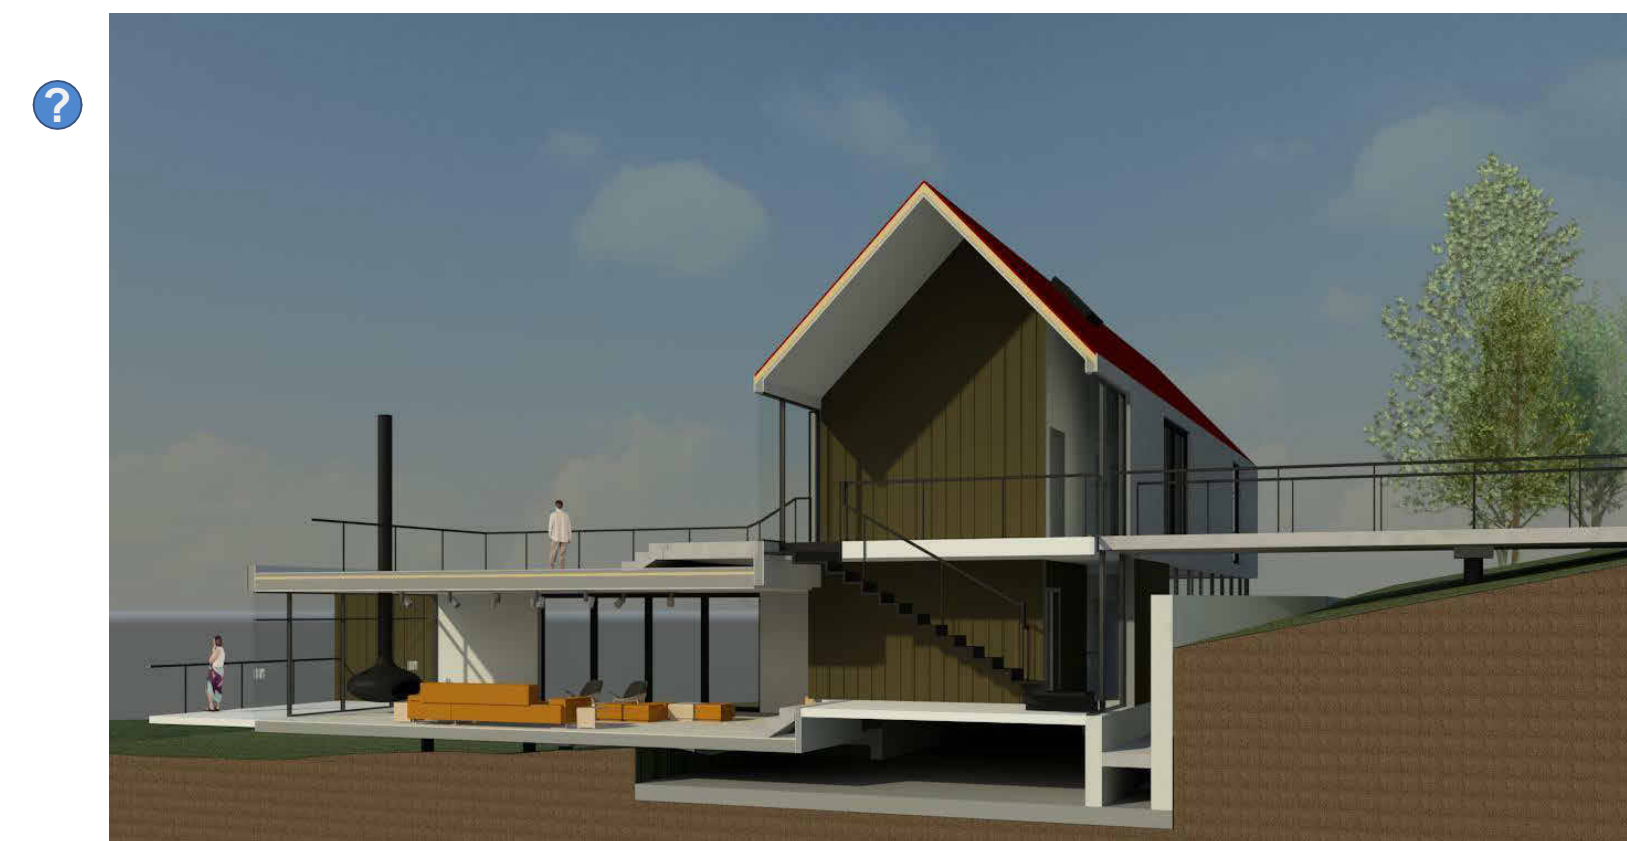


To learn more about the contents of the sample project look for the Help Icon  near an element. Select the icon and then select the Learning Link parameter in the properties palette. Use the "..." to connect to the related wiki topic. Once you have reviewed the wiki topic select the content reviewed check box in the properties palette.

Level	Topic	What view	Reviewed?
01 - Basic	Add levels to the project.	Elevations - East	No
01 - Basic	Place grids into a project and control grid heads display.	Floor Plan Level 1	No
01 - Basic	Place walls and doors into your project.	Floor Plan Level 1	No
01 - Basic	Add doors to the project.	Floor Plan Level 2	No
01 - Basic	Add a window to the project.	Floor Plan Level 2	No
01 - Basic	Add floors to the project	Sections - Building Section	No
01 - Basic	Create a roof.	Sections - Building Section	No
01 - Basic	Create a stair by sketching boundaries and risers.	Floor Plan Level 1	No
01 - Basic	Create a curtain wall.	Floor Plan Level 1	No
01 - Basic	Create a frestanding railing.	Elevation - East	No
01 - Basic	Add plants and entourage to the project.	Floor Plan - Site	No
01 - Basic	Create section views.	Floor Plan Level 1	No
01 - Basic	Add a callout	Sections - Building Section	No
01 - Basic	Create a detail view.	Sections (Wall Section) - Typ. Wall Section	No
01 - Basic	Set the scale of a view.	Sections (Wall Section) - Typ. Wall Section	No
01 - Basic	Specify the detail level of a view	Sections (Wall Section) - Typ. Wall Section	No
01 - Basic	Add a detail component to a view.	Detail Views - Typ. Wall Roof Connection	No
01 - Basic	Add detail,ines to a view.	Detail Views - Typ. Wall Roof Connection	No
01 - Basic	Add aligned dimensions to a view.	Floor Plan Level 1	No
01 - Basic	Add text notes to a view.	Floor Plan Level 1	No
01 - Basic	Add a sheet to the project.	Sheet - A001	No
01 - Basic	Add views to a sheet.	Sheet - A102	No
02 - Intermediate	Create a topographic surface.	Floor Plans - Site	No
02 - Intermediate	Add a building pad to a toposurface.	Floor Plans - Site	No
02 - Intermediate	Create an element with compound structure.	Sections - Building Section	No
02 - Intermediate	Add a dor to a curtain wall.	Floor Plan Level 2	No
02 - Intermediate	Add Property lines to a site plan.	Floor Plans - Site	No
02 - Intermediate	Create a schedule.	Sheet - A101	No
02 - Intermediate	Offset level head from the level line.	Elevations - East	No
02 - Intermediate	Control the size of a view.	Sheets - A001	No
02 - Intermediate	Add insulation in a detail view.	Detail Views - Typ. Wall Roof Connection	No
02 - Intermediate	Create renderings.	Sheet - A001	No
03 - Advanced	Create a 3d section view.	Sheet - A001	No
03 - Advanced	Create a color scheme for a view.	Floor Plan Level 2	No
03 - Advanced	Add a color fill legend.	Floor Plan Level 2	No
03 - Advanced	Control the cut and projected lineweights of elements.	Sections - Building Section	No
03 - Advanced	Assign a color gradient as a background.	Elevations - East	No
03 - Advanced	Control the way the site looks in section.	Elevation - East	No
03 - Advanced	Adjust rendered image exposure.	Sheet - A001	No
03 - Advanced	Use the sun path.	Sheet - A101	No

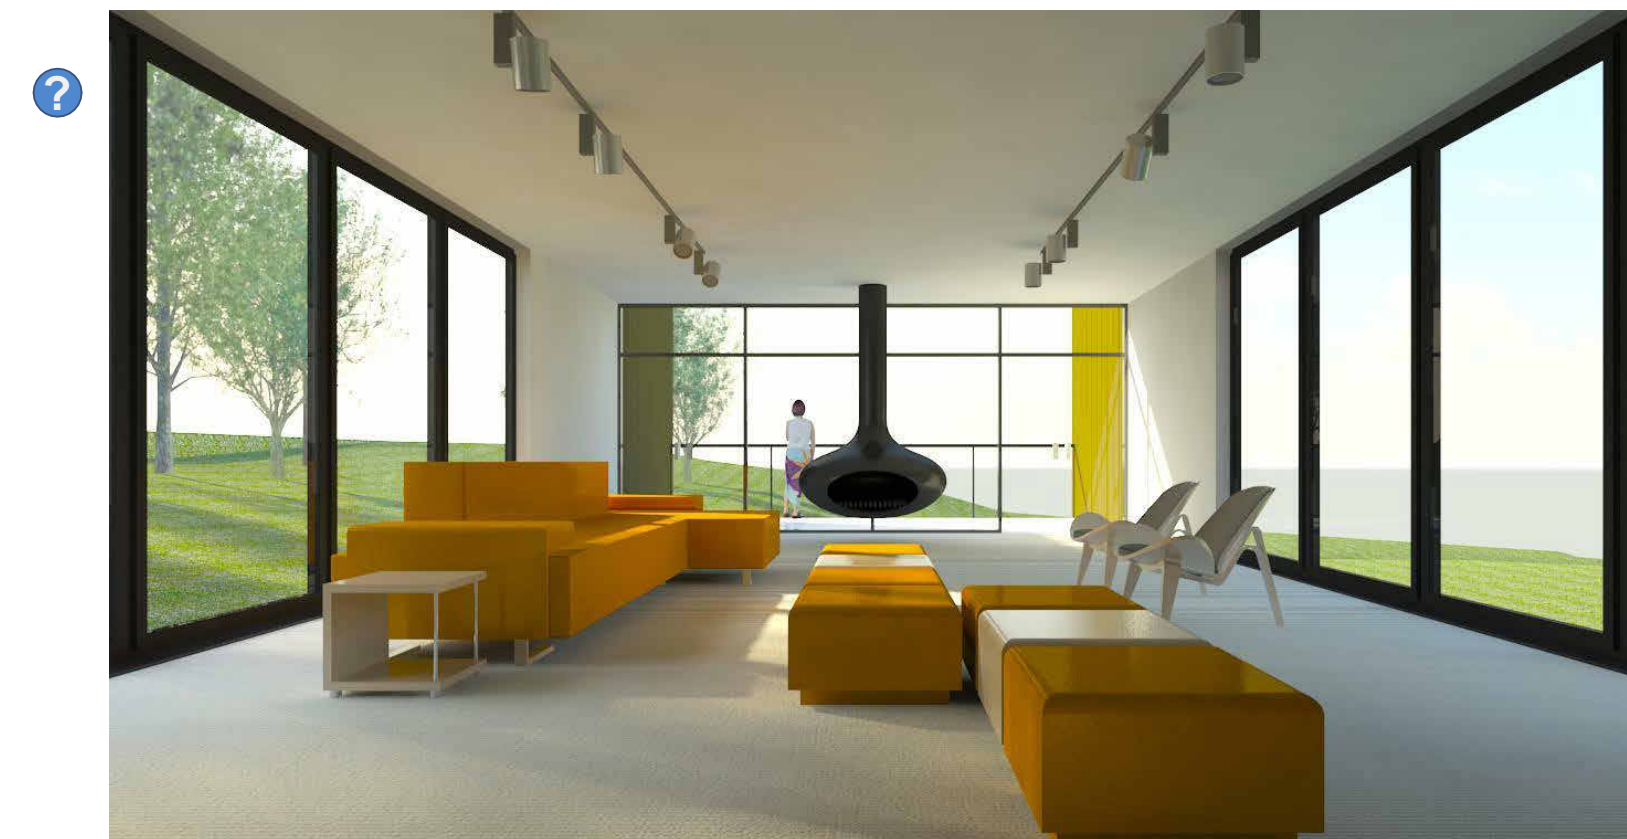

Consultant
Address
Address
Phone
Fax
e-mail

Consultant
Address
Address
Phone
Fax
e-mail

Consultant
Address
Address
Phone
Fax
e-mail

Consultant
Address
Address
Phone
Fax
e-mail

[illegible]

Autodesk
Sample House

Title Sheet

Project number	001-00
----------------	--------

Date	Issue Date
------	------------

Drawn by SM

Checked by JLH

A001

Scale 1 : 1






Consultant
Address
Address
Phone
Fax
e-mail


Consultant
Address
Address
Phone
Fax
e-mail

Consultant
Address
Address
Phone
Fax
e-mail

Consultant
Address
Address
Phone
Fax
e-mail

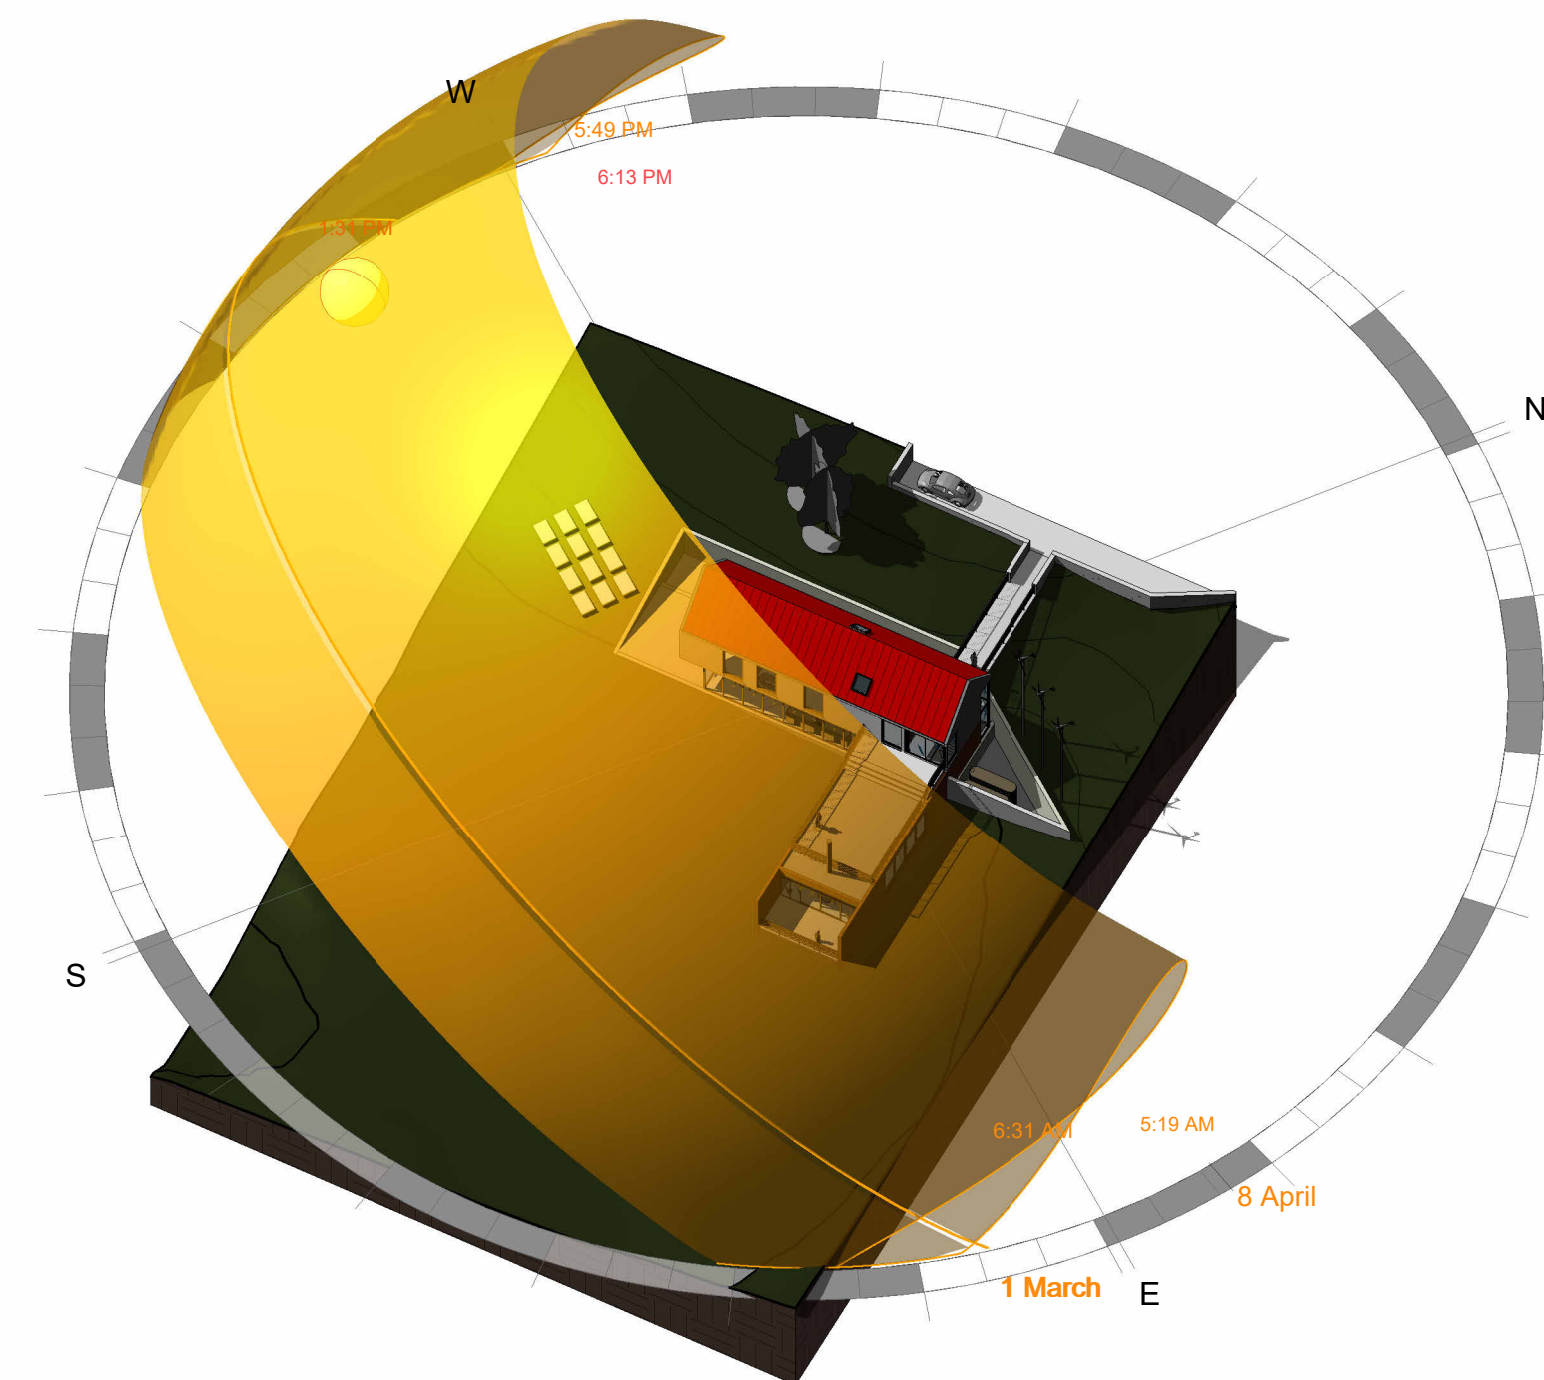

2 Solar Analysis

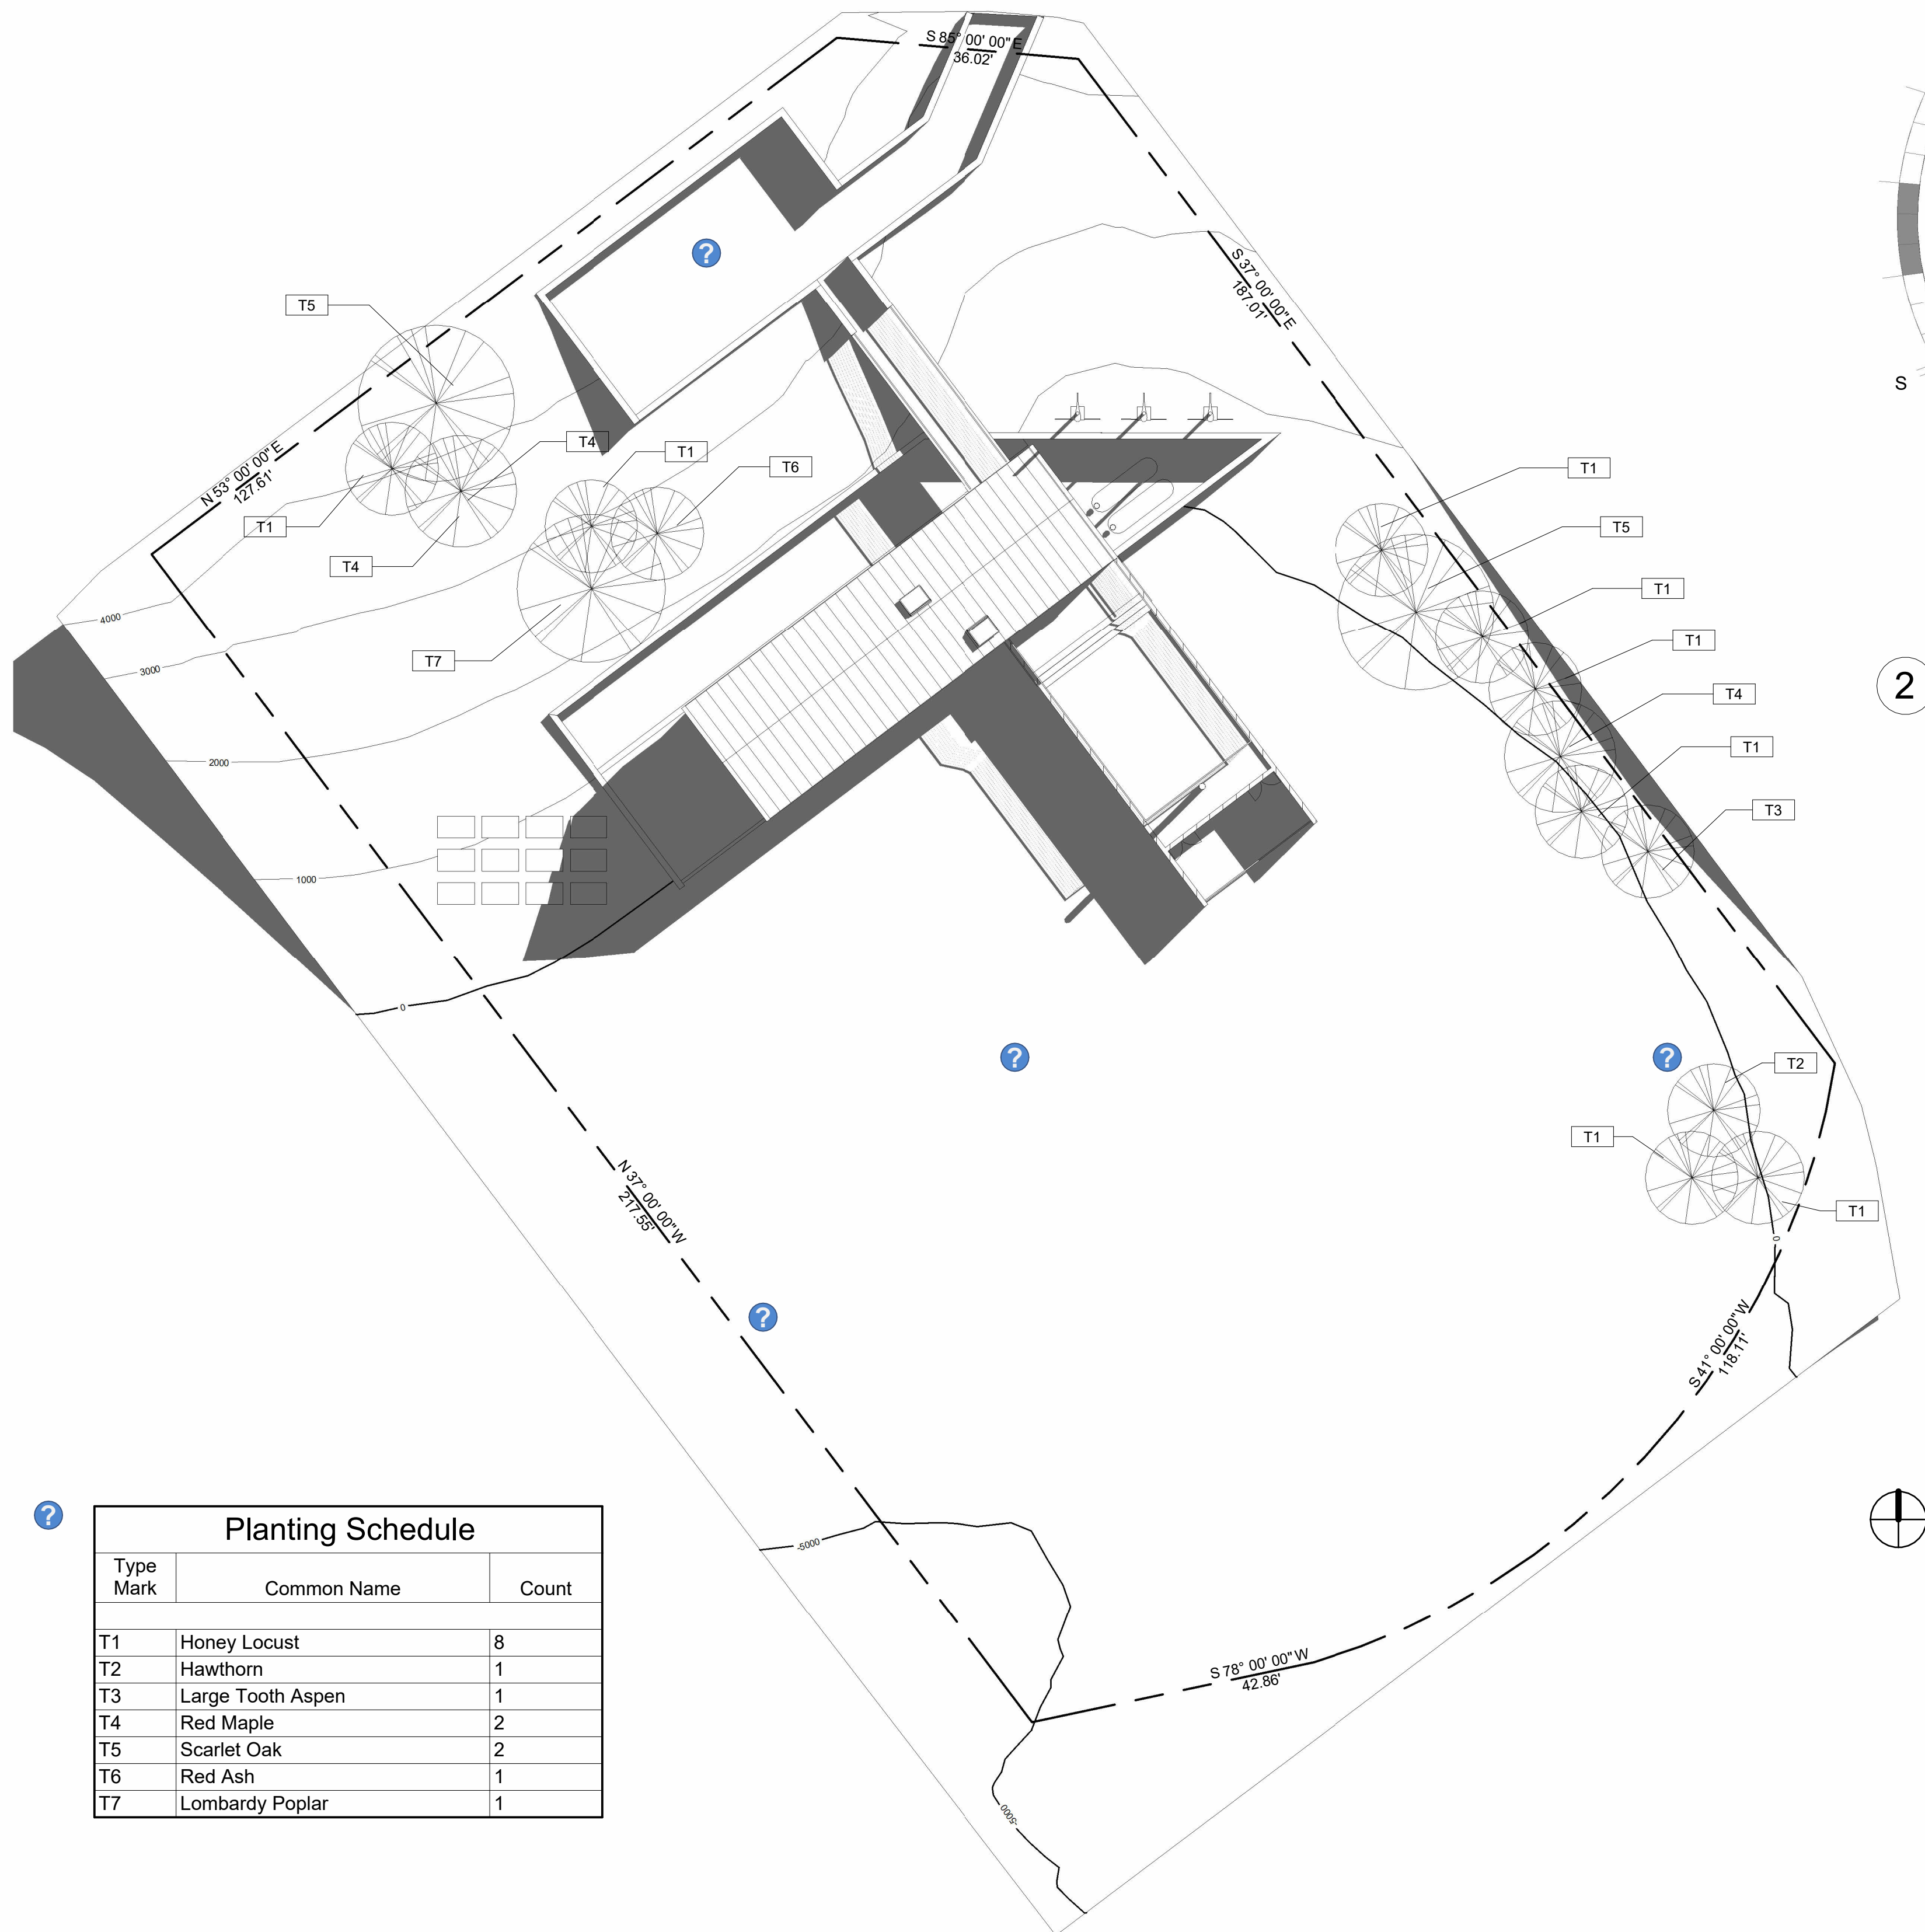

Planting Schedule		
Type Mark	Common Name	Count
T1	Honey Locust	8
T2	Hawthorn	1
T3	Large Tooth Aspen	1
T4	Red Maple	2
T5	Scarlet Oak	2
T6	Red Ash	1
T7	Lombardy Poplar	1

1 Site
1 : 200

[illegible]

Autodesk
Sample House

Site Plan

Project number	001-00
----------------	--------




Date	Issue Date
------	------------

Drawn by SM


Checked by JLH

A101

Scale	1 : 200
-------	---------

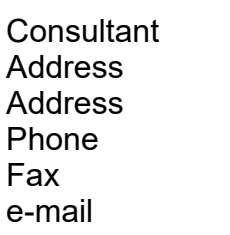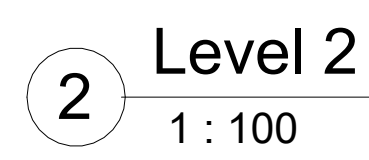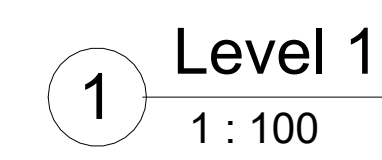


Scale	1 : 100
-------	---------

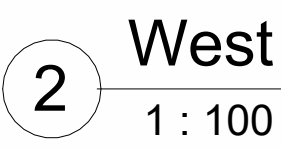

1 Building Section
1 : 100

4 Typical Wall Roof Connection

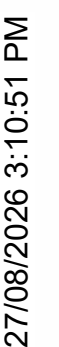



Consultant
Address
Address
Phone
Fax
e-mail

Consultant
Address
Address
Phone
Fax
e-mail

[illegible]

Scale	As indicated
-------	--------------

22/08/2026 3:11:07 PM

