

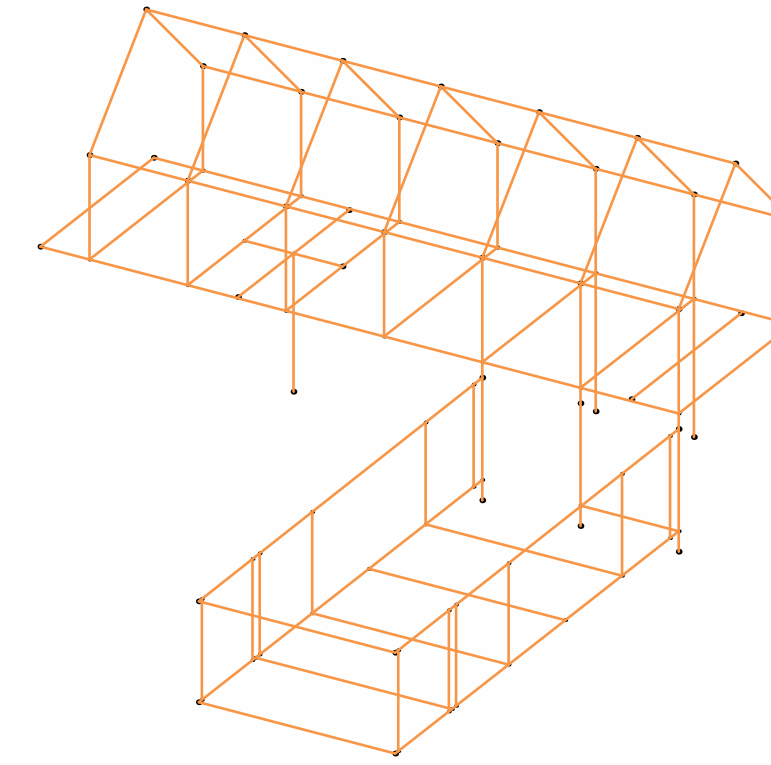



Autodesk® Revit® Basic Structural Sample Project

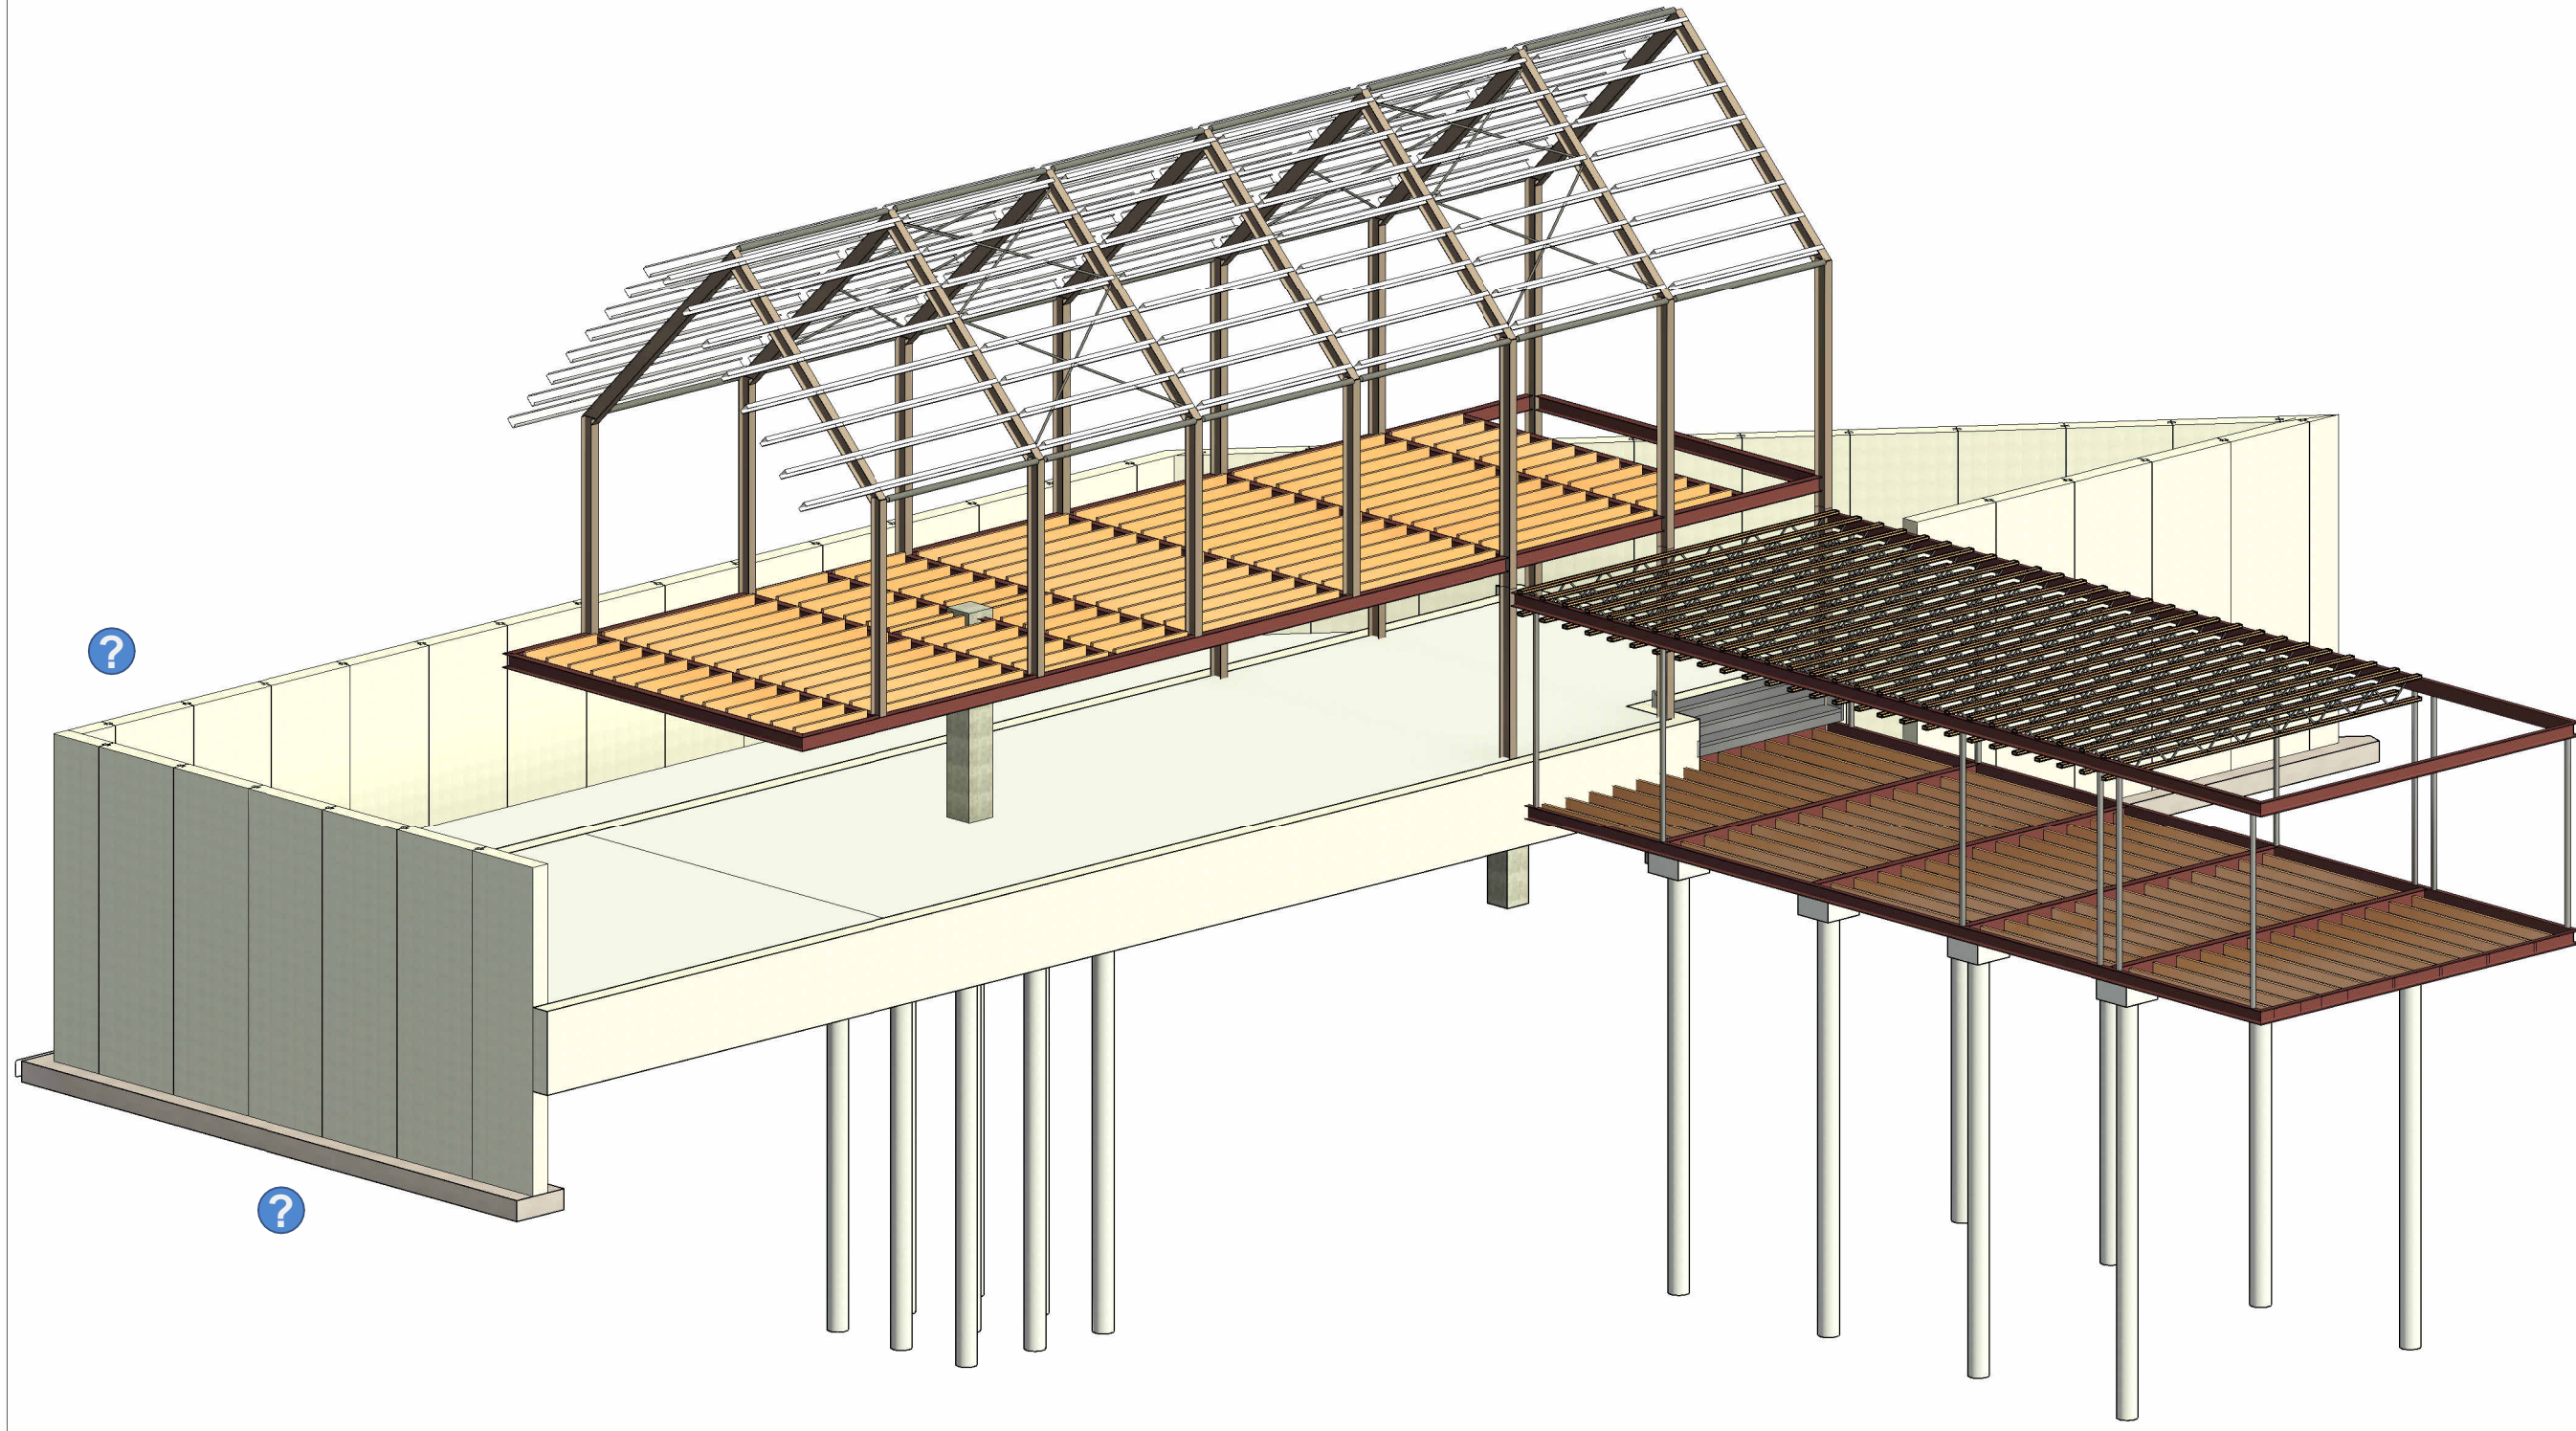

4 Analytical Model

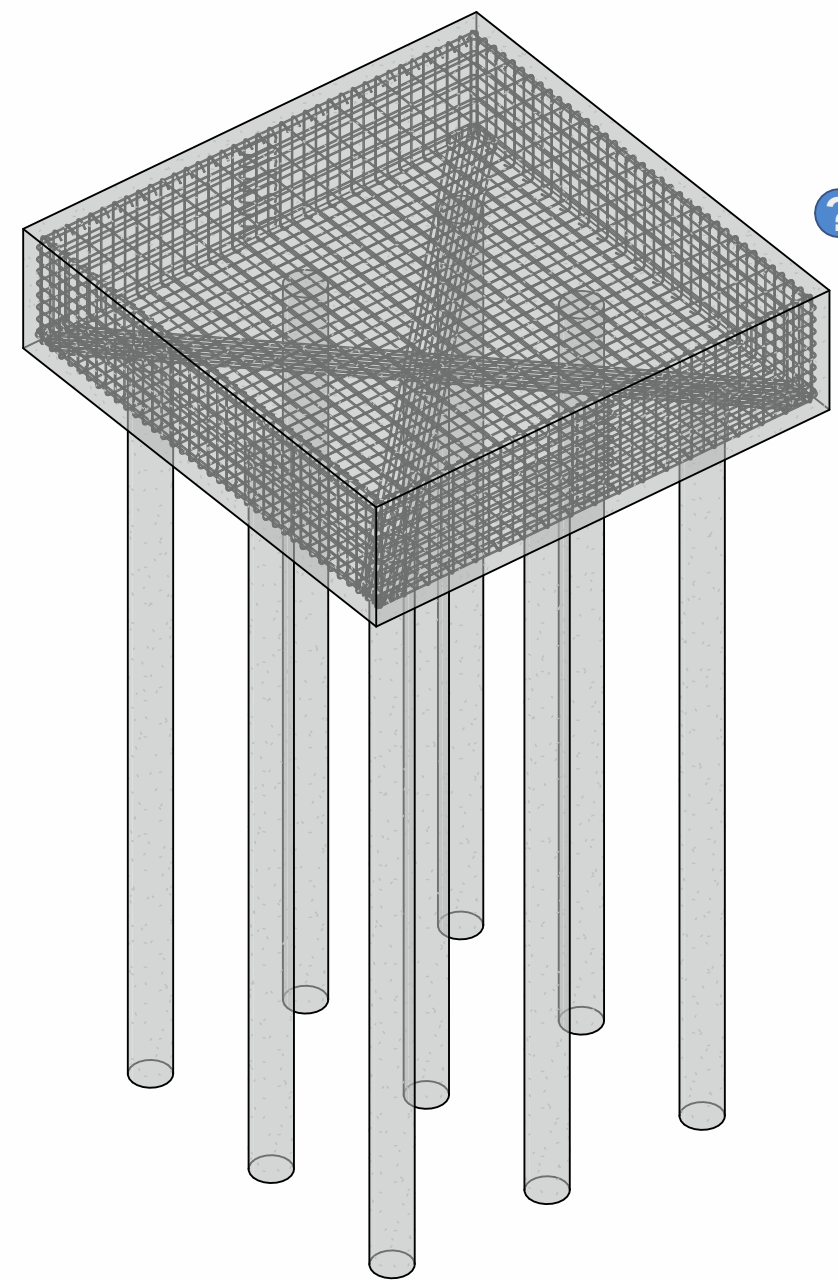

2 Central Pile

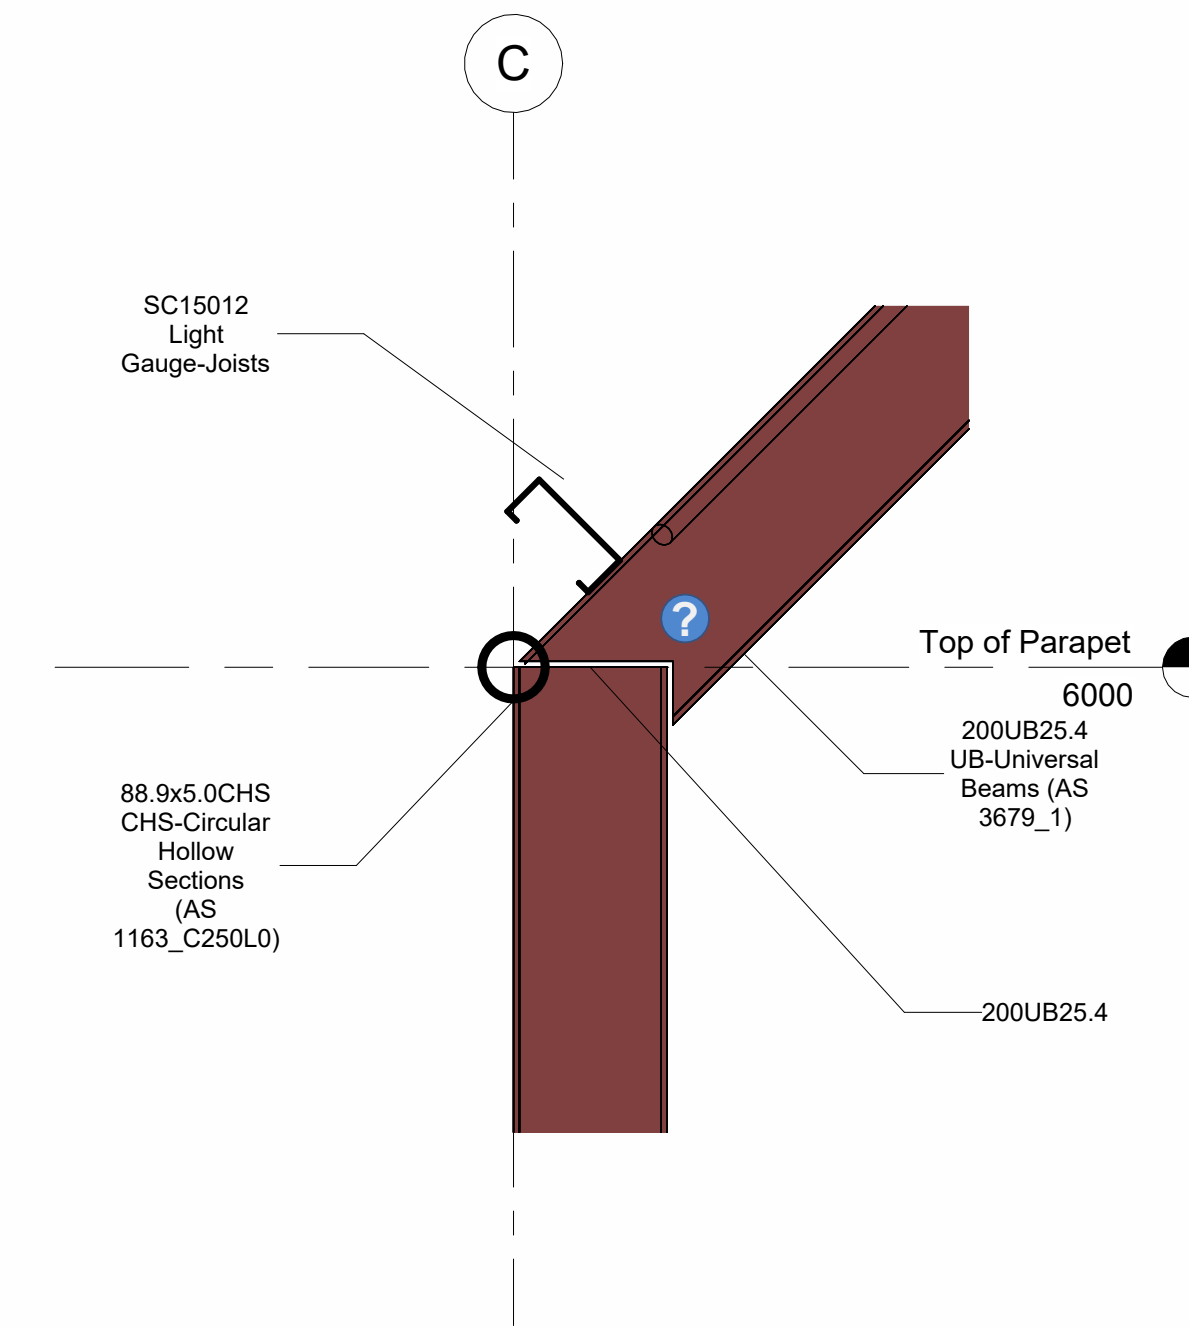

3 Framing - Detail
1 : 10

Level	Topic	What View	Reviewed?
01 - Basic	Add levels to the project.	Elevations - South	No
01 - Basic	Place grids into a project and control grid heads display.	Structural Plans - Level 1	No
01 - Basic	Add a Column	Structural Plans - Level 2	No
01 - Basic	Add a Beam	Sections - Longitudinal Section	No
01 - Basic	Create Structural Wall	Sheet - S202	No
01 - Basic	Place Beam Tags	Sections - Longitudinal Section	No
01 - Basic	Add floors to the project	Sections - Cross Section	No
01 - Basic	Create Wall Footing	Sheet - S202	No
01 - Basic	Create section views.	Sections - Longitudinal Section	No
01 - Basic	Add a callout	Sections - Cross Section	No
01 - Basic	Create a detail view.	Sections - Cross Section	No
01 - Basic	Create 3D View	Sheet - S001	No
01 - Basic	Set the scale of a view.	Roof Peak	No
01 - Basic	Specify the detail level of a view	Elevations - South	No
01 - Basic	Add detail lines to a view.	Drafting Views - Pile Cap Detail	No
01 - Basic	Add aligned dimensions to a view.	Structural Plans - Level 1	No
01 - Basic	Add text notes to a view.	Drafting Views - Pile Cap Detail	No
01 - Basic	Add a sheet to the project.	Sheet - S001	No
02 - Intermediate	Offset level head from the level line.	Elevations - South	No
02 - Intermediate	Copy/Monitor Elements from a linked model	Structural Plans - Level 1	No
02 - Intermediate	Create Beam System	Structural Plans - Level 1	No
02 - Intermediate	Create a schedule.	Sheet - S206	No
02 - Intermediate	Create Graphical Column Schedule	Sheet - S206	No
02 - Intermediate	Place Rebar	Structural Plans - Level 1	No
02 - Intermediate	Cut an Opening in a Framing Element	Sheet - S001	No
02 - Intermediate	Import DWG Details	Sheet - S204	No
02 - Intermediate	Make Elements Transparent	Sheet - S001	No
03 - Advanced	Structural Analytical Model	Sheet - S001	No
03 - Advanced	Create Parts	Sheet - S001	No



www.autodesk.com/revit

Consultant
Address
Address
Phone
Fax
e-mail

Consultant
Address
Address
Phone
Fax
e-mail

Consultant
Address
Address
Phone
Fax
e-mail

Consultant
Address
Address
Phone
Fax
e-mail

[illegible]

Autodesk

Sample House

Title Sheet

Project number	001-00
----------------	--------


Date	Issue Date
------	------------

Drawn by AA


Checked by JLH

S001

Scale 1 : 10

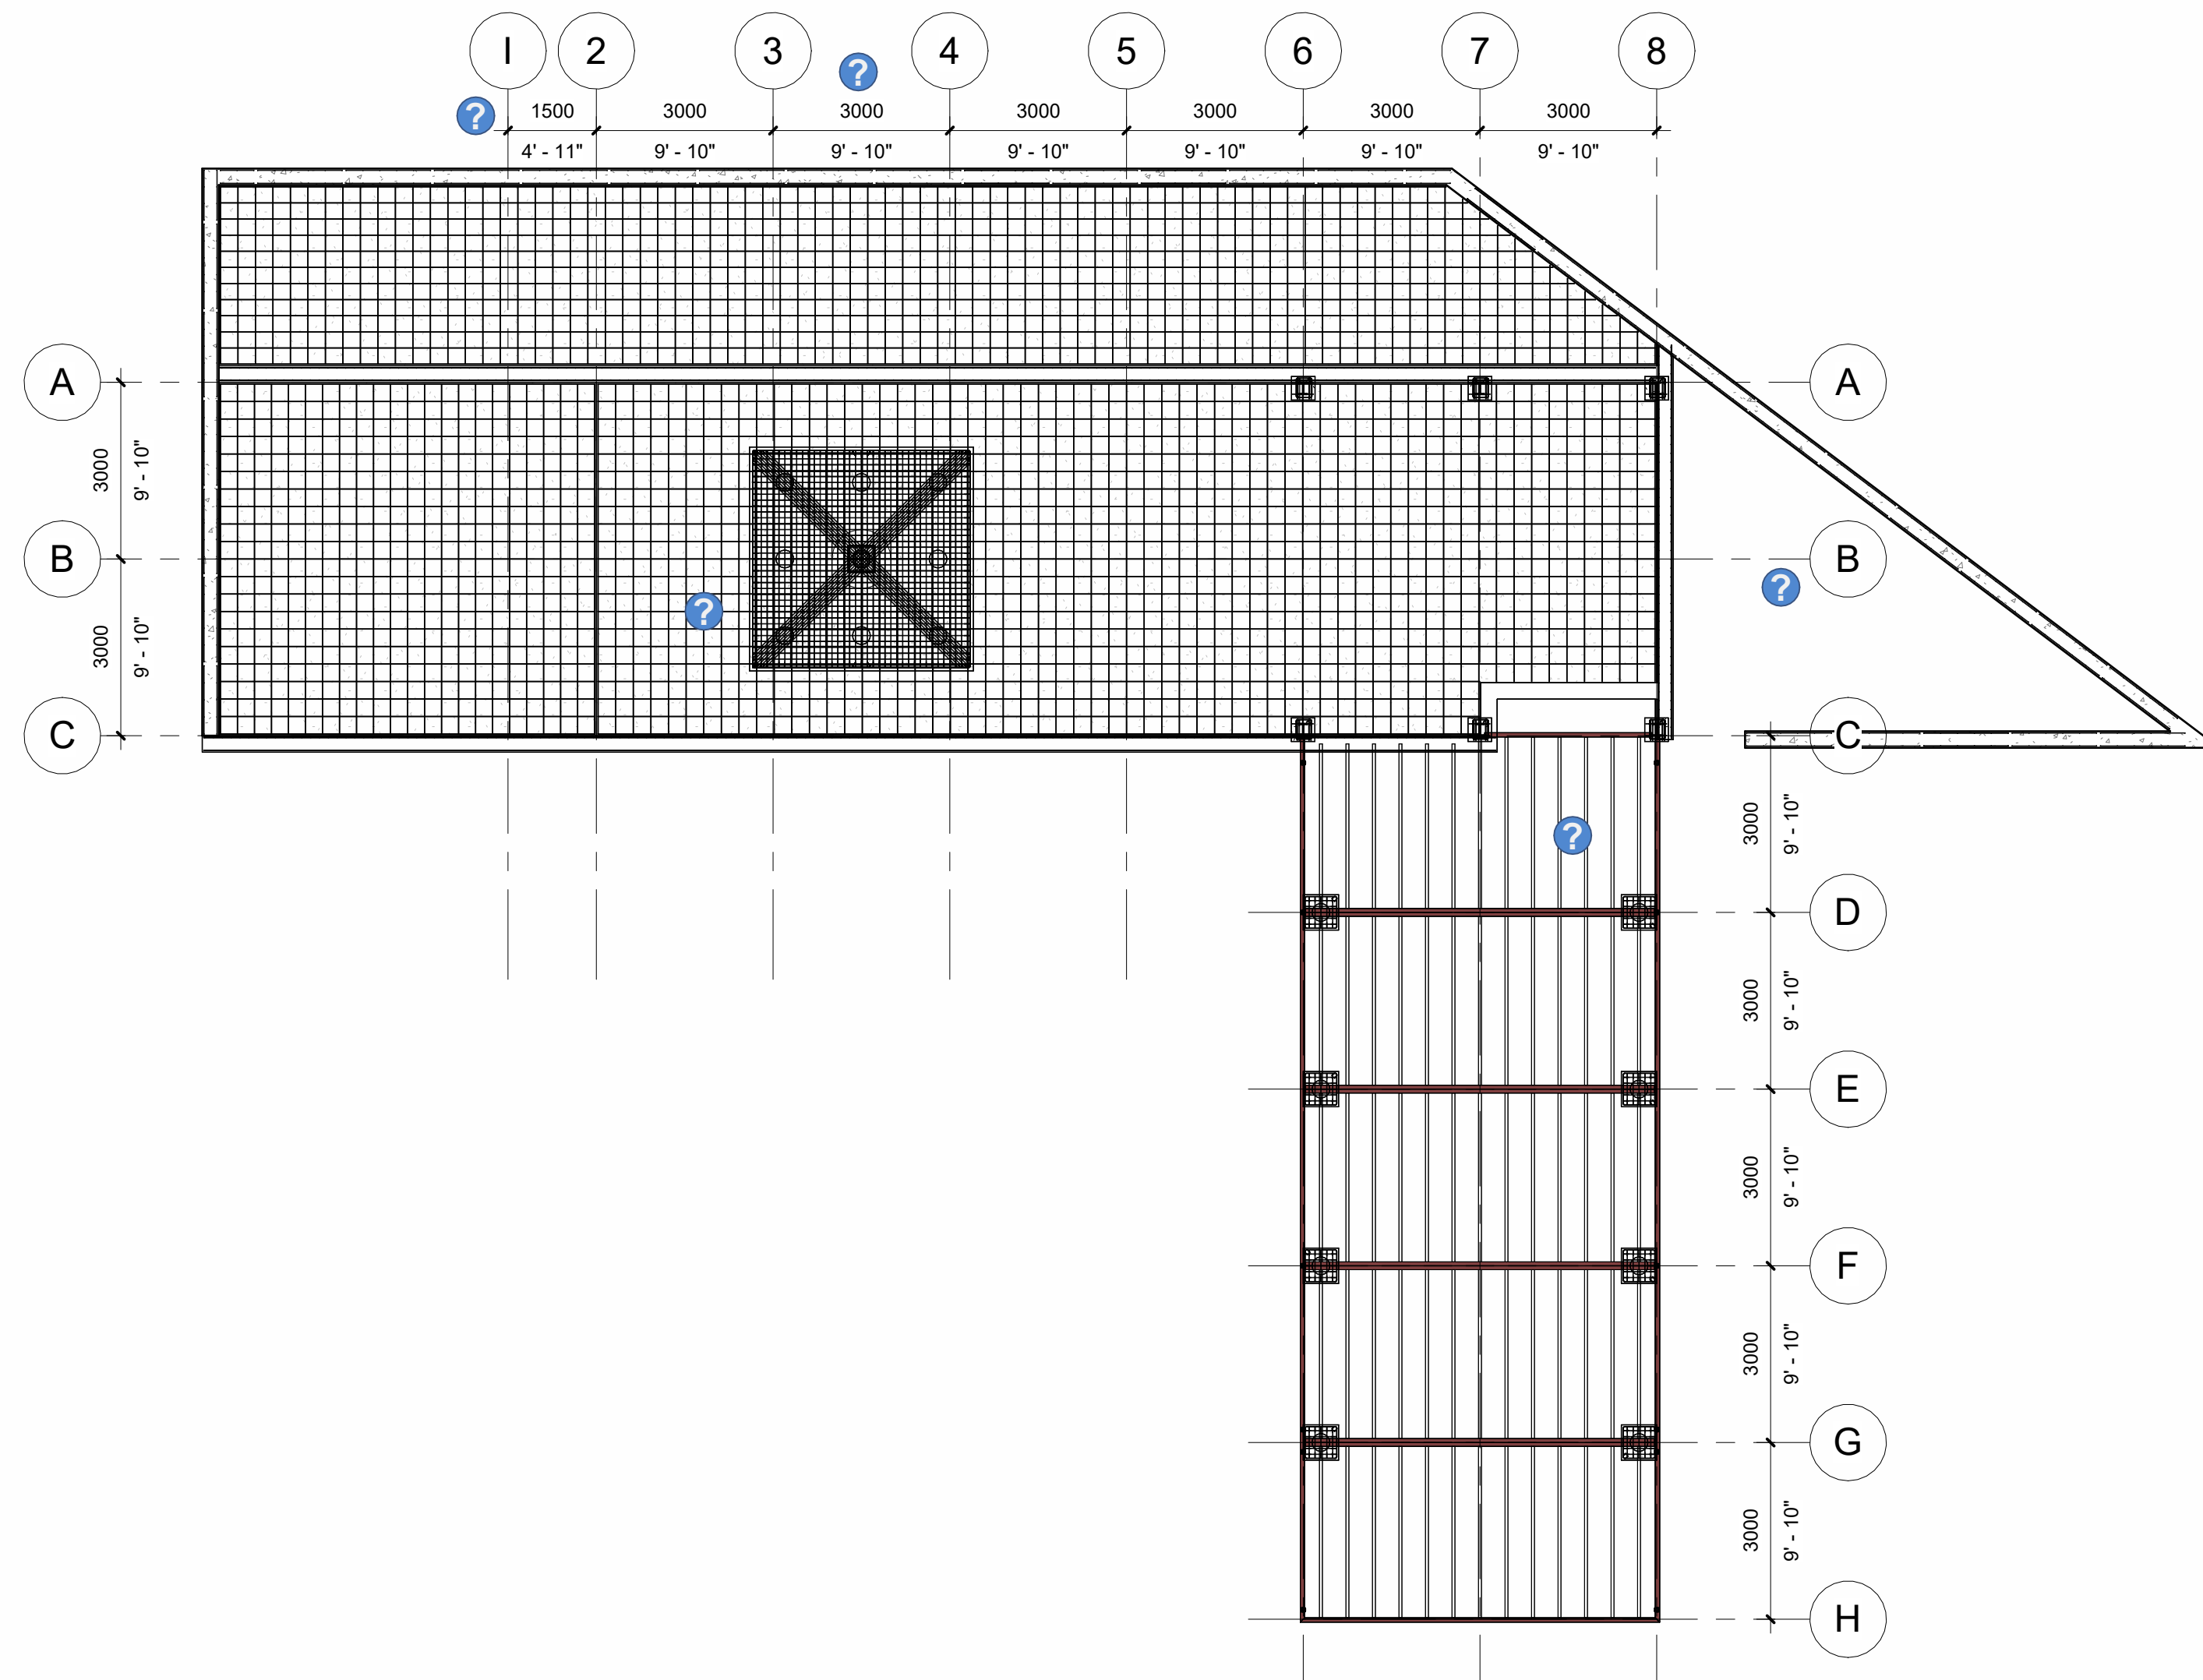

1 Level 1
1 : 100

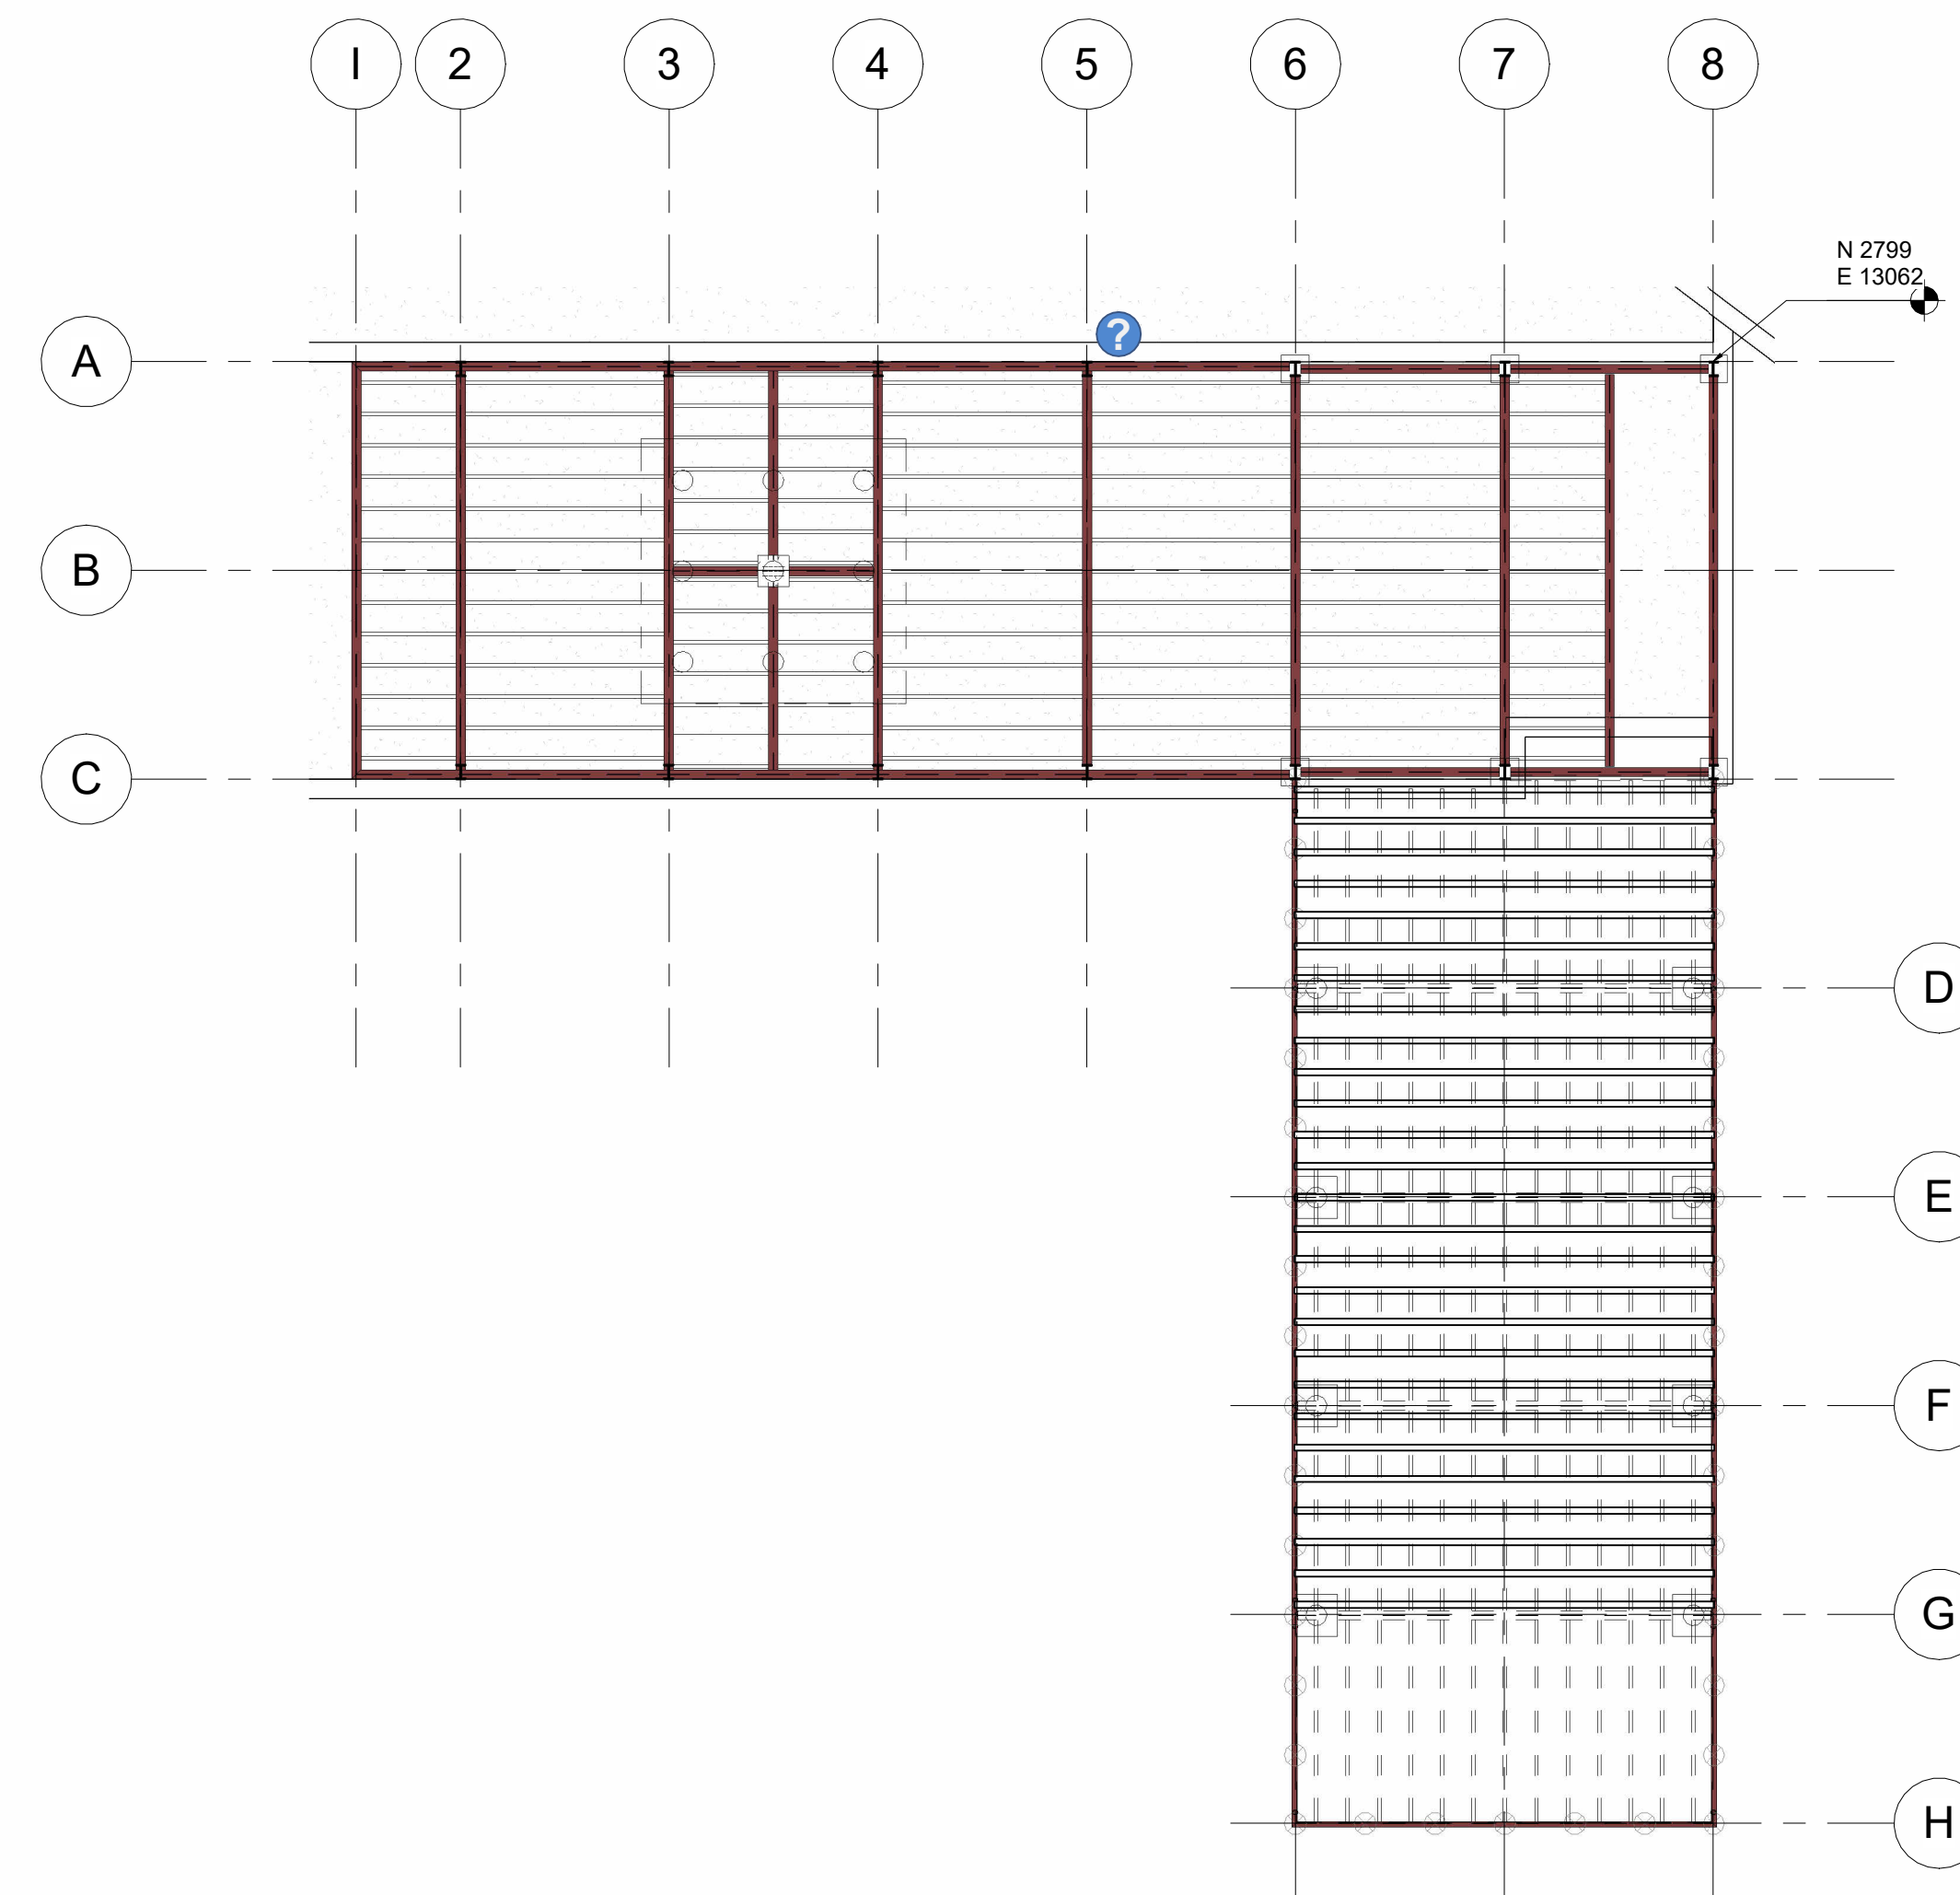

2 Level 2
1 : 100



www.autodesk.com/revit

Consultant
Address
Address
Phone
Fax
e-mail

Consultant
Address
Address
Phone
Fax
e-mail

Consultant
Address
Address
Phone
Fax
e-mail

Consultant
Address
Address
Phone
Fax
e-mail

[illegible]

Autodesk

Sample House

Framing Plans

Project number	001-00
----------------	--------

Date	Issue Date
------	------------

Drawn by	Author
----------	--------


Checked by	Checker	:
------------	---------	---

S101

Scale	1 : 100
-------	---------



2 Cross Section
1 : 50

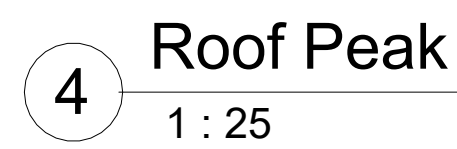

www.autodesk.com/revit

Consultant
Address
Address
Phone
Fax
e-mail

Consultant
Address
Address
Phone
Fax
e-mail

Consultant
Address
Address
Phone
Fax
e-mail

Consultant
Address
Address
Phone
Fax
e-mail

[illegible]

Autodesk

Sample House

Upper House Framing

Project number	001-00
----------------	--------



Date	Issue Date
------	------------

Drawn by	Author
----------	--------

Checked by	Checker	:
------------	---------	---

S201

Scale	As indicated
-------	--------------

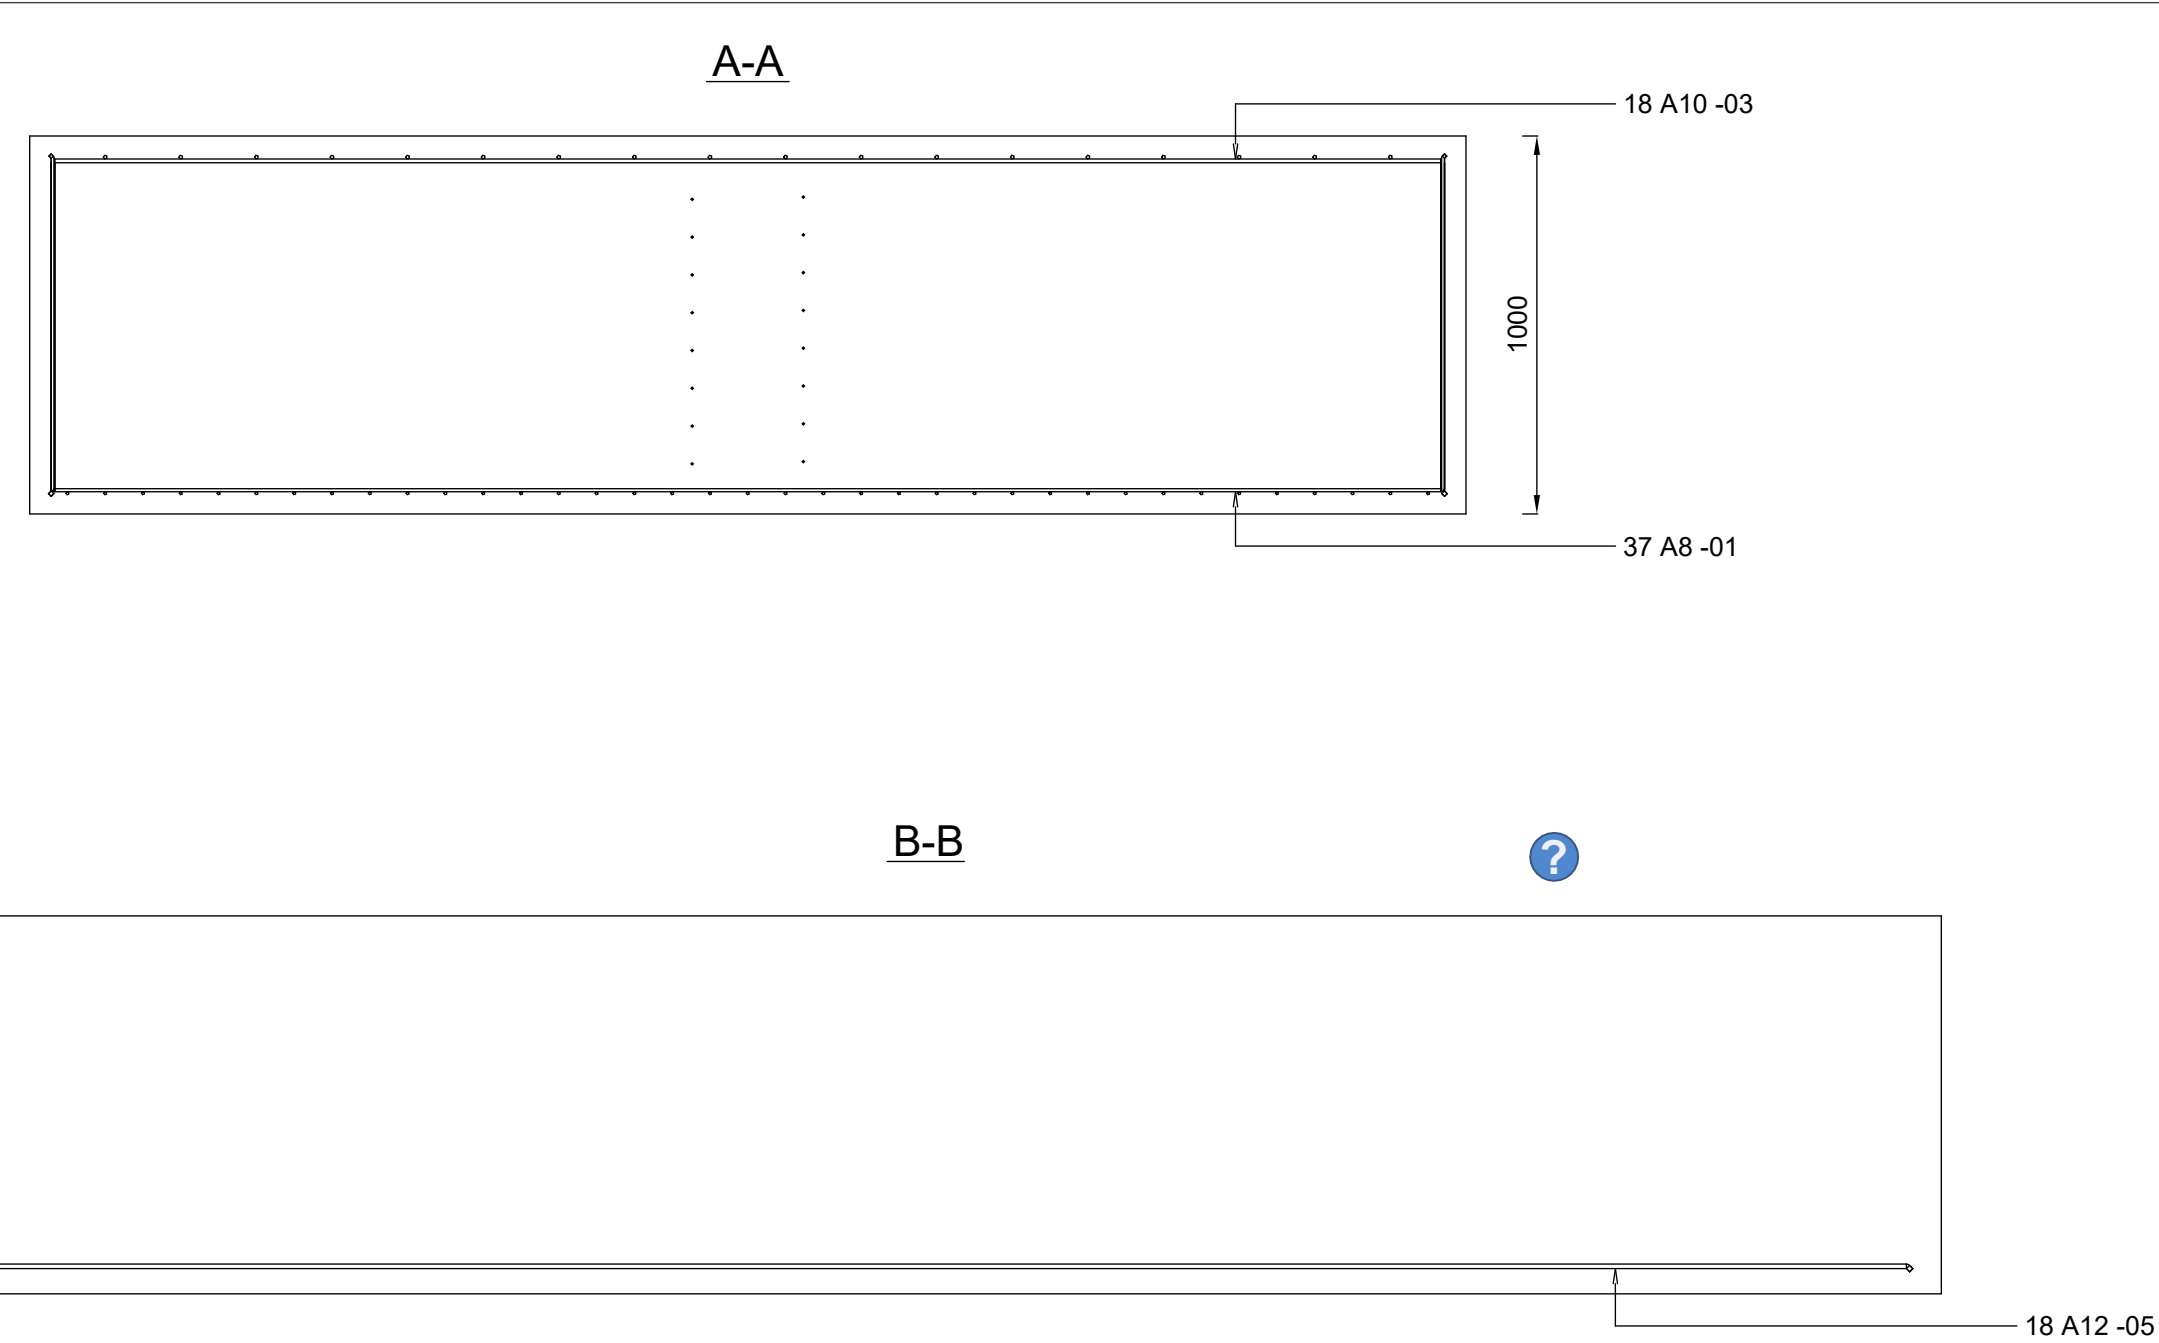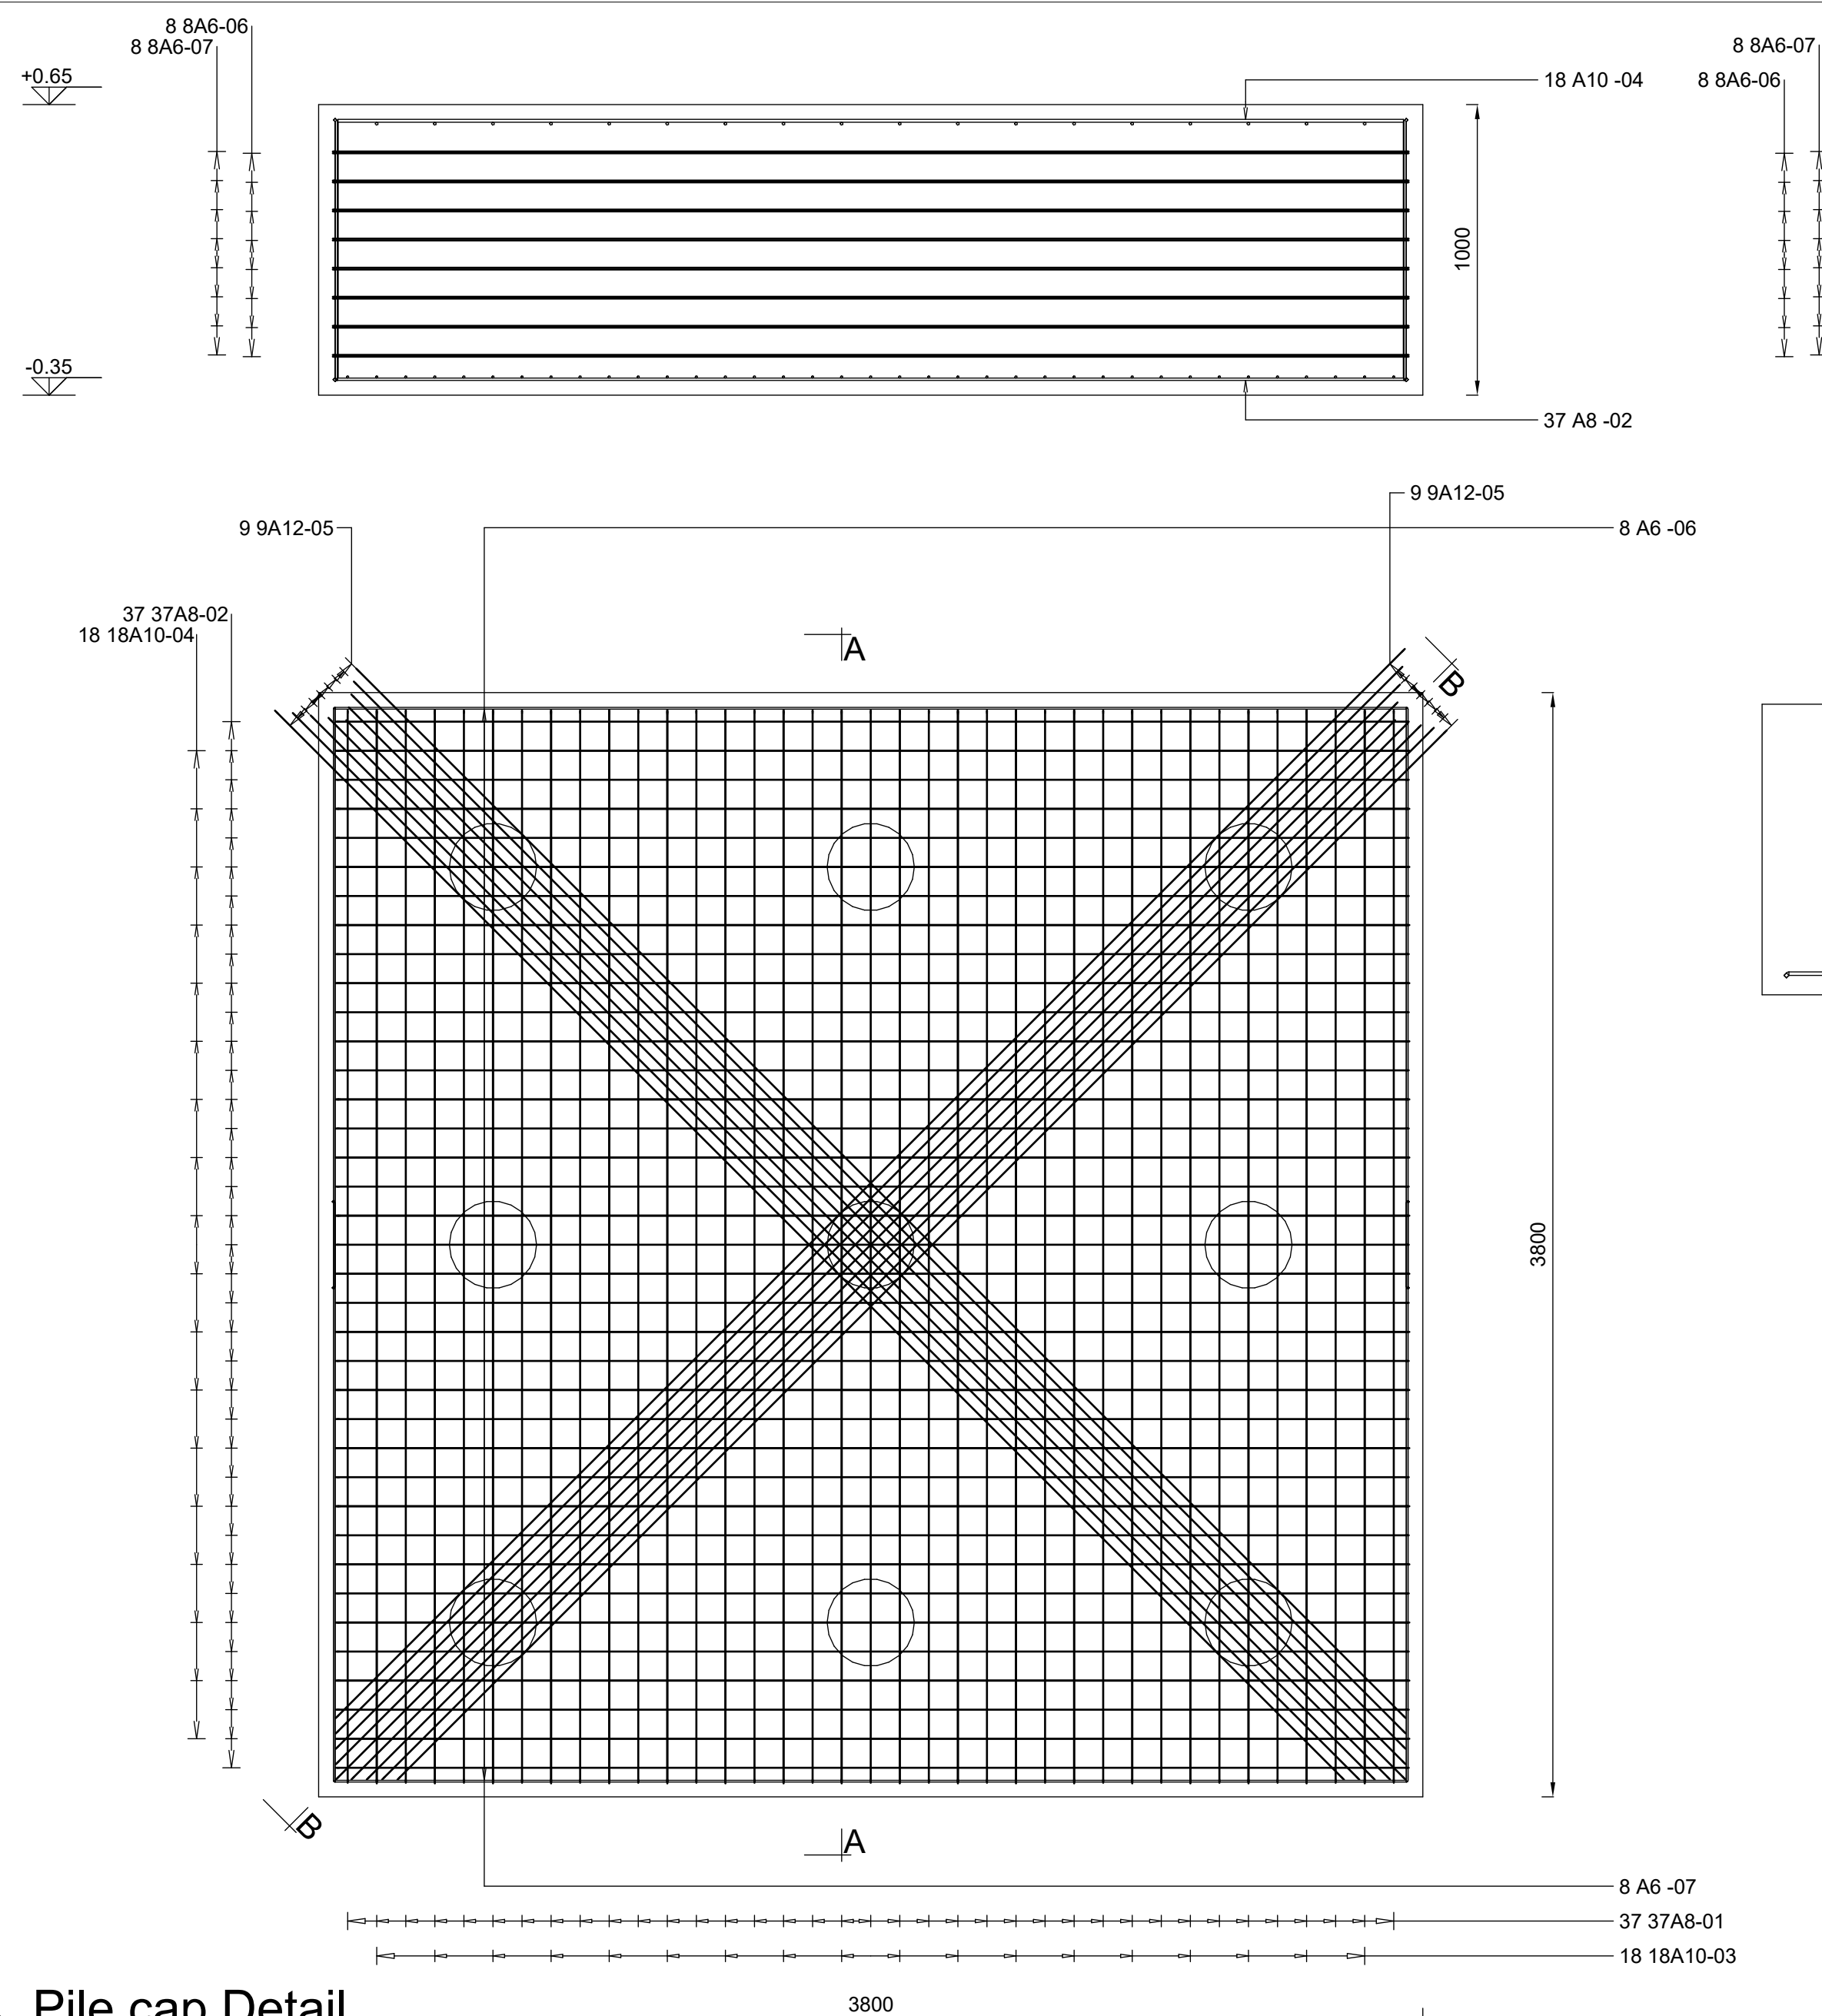

? Pile cap (1175183)
 Position: 1.1.1
 Number of elements: 1



www.autodesk.com/revit

Consultant
Address
Address
Phone
Fax
e-mail

Consultant
Address
Address
Phone
Fax
e-mail

Consultant
Address
Address
Phone
Fax
e-mail

Consultant
Address
Address
Phone
Fax
e-mail

[illegible]

Autodesk

Sample House

Central Pile Section

Project number	001-00
----------------	--------



Date	Issue Date
------	------------

Drawn by	Author
----------	--------

Checked by	Checker
------------	---------

S203


Scale	As indicated
-------	--------------

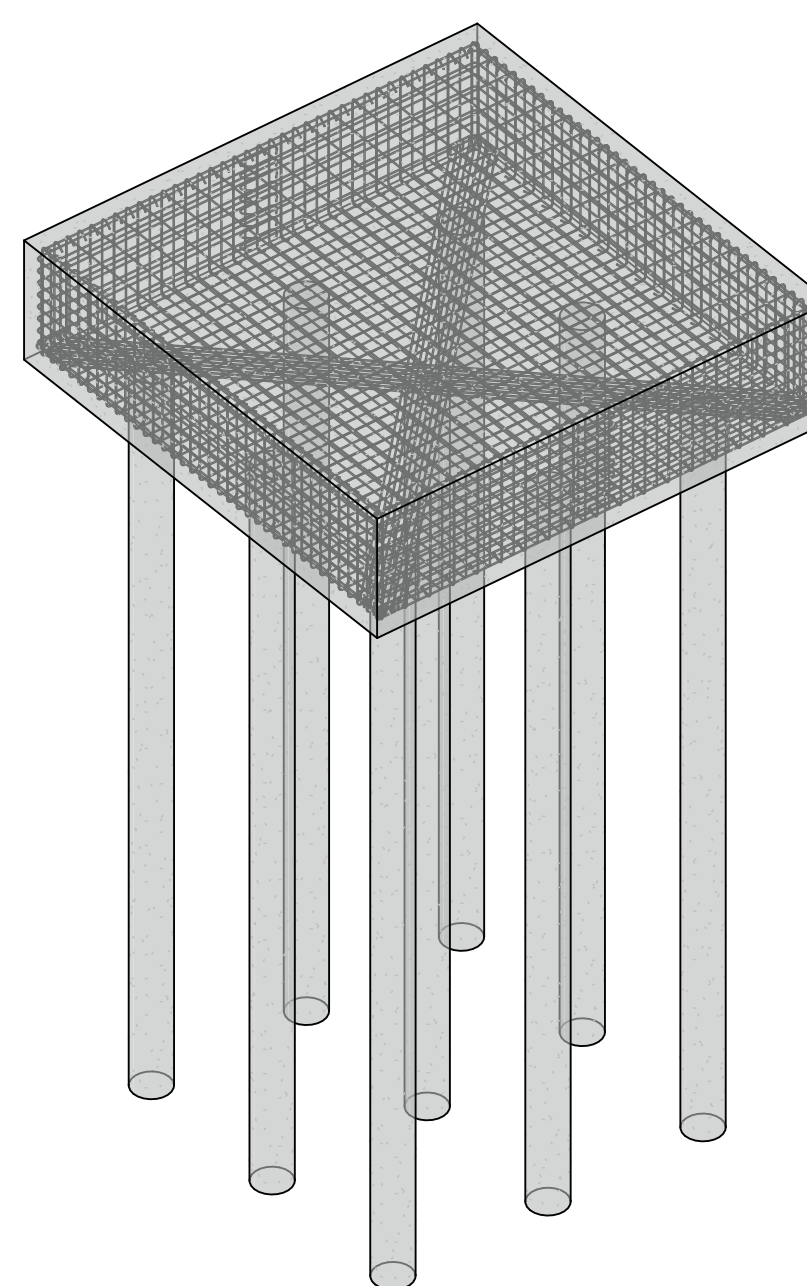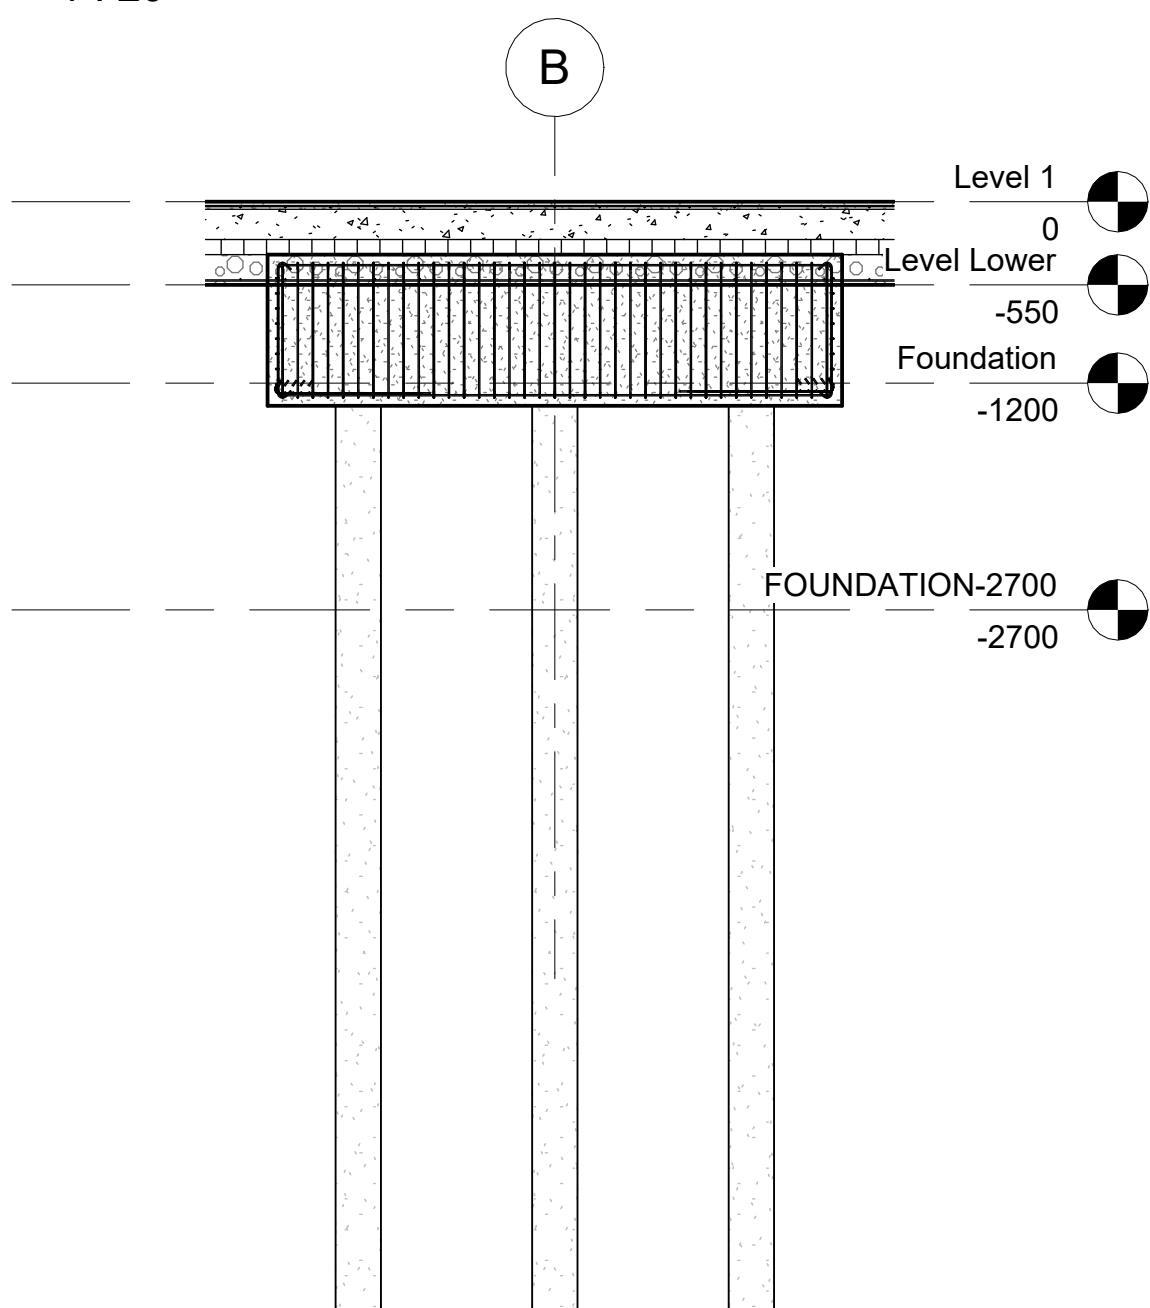

Position: 1.1.1
Number of elements: 1



Member		Bar mark	Type and Size	Number		Length (mm)	Shape code	A (mm)	B (mm)	C (mm)	D (mm)	E/R (mm)	Rev.
Name	Num			in the elem.	total								
Continuous footing (1178029)	1	01	X8	52	52	2375	31	250	850	250	850		
		02	X8	3	3	20650		20655					
		03	X8	3	3	20650		20655					


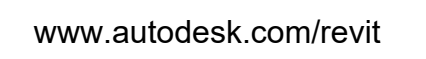


Consultant
Address
Address
Phone
Fax
e-mail

Consultant
Address
Address
Phone
Fax
e-mail

1 Continuous Footing

Spread footing (1177820)
(F)
Scale 1 : 20

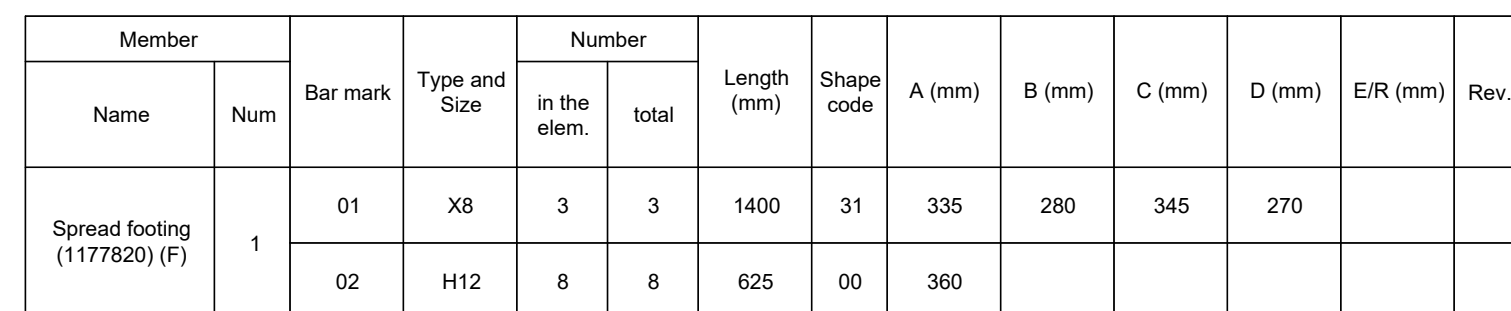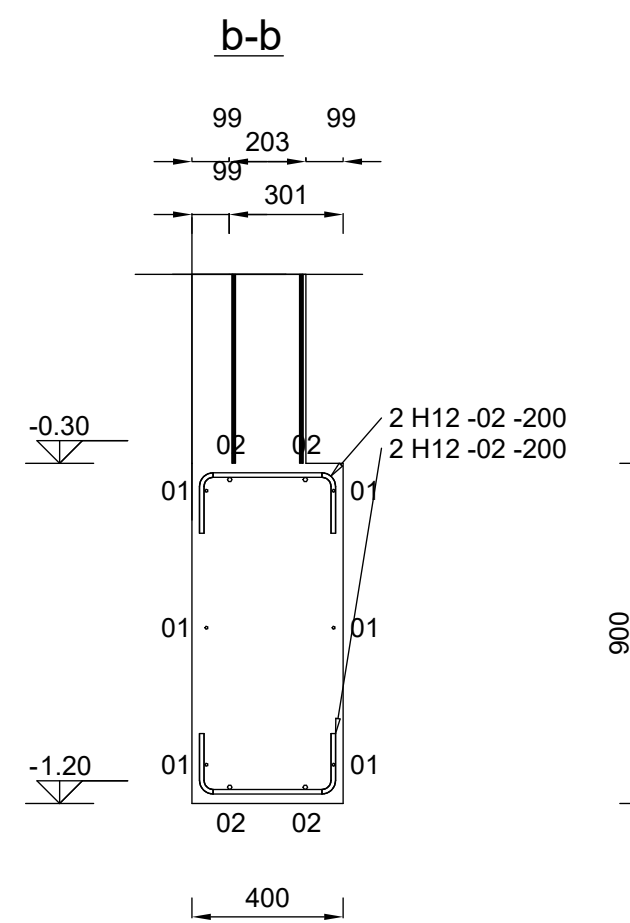

2 Spread Footing

[illegible]

Footing Detail

Checked by	Checker
------------	---------

Scale	As indicated
-------	--------------





Consultant
Address
Address
Phone
Fax
e-mail


Consultant
Address
Address
Phone
Fax
e-mail


Scale	1 : 100
-------	---------


22/08/2026 2:14:26 PM

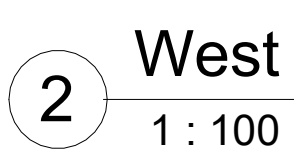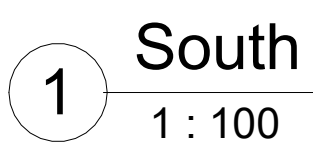



B

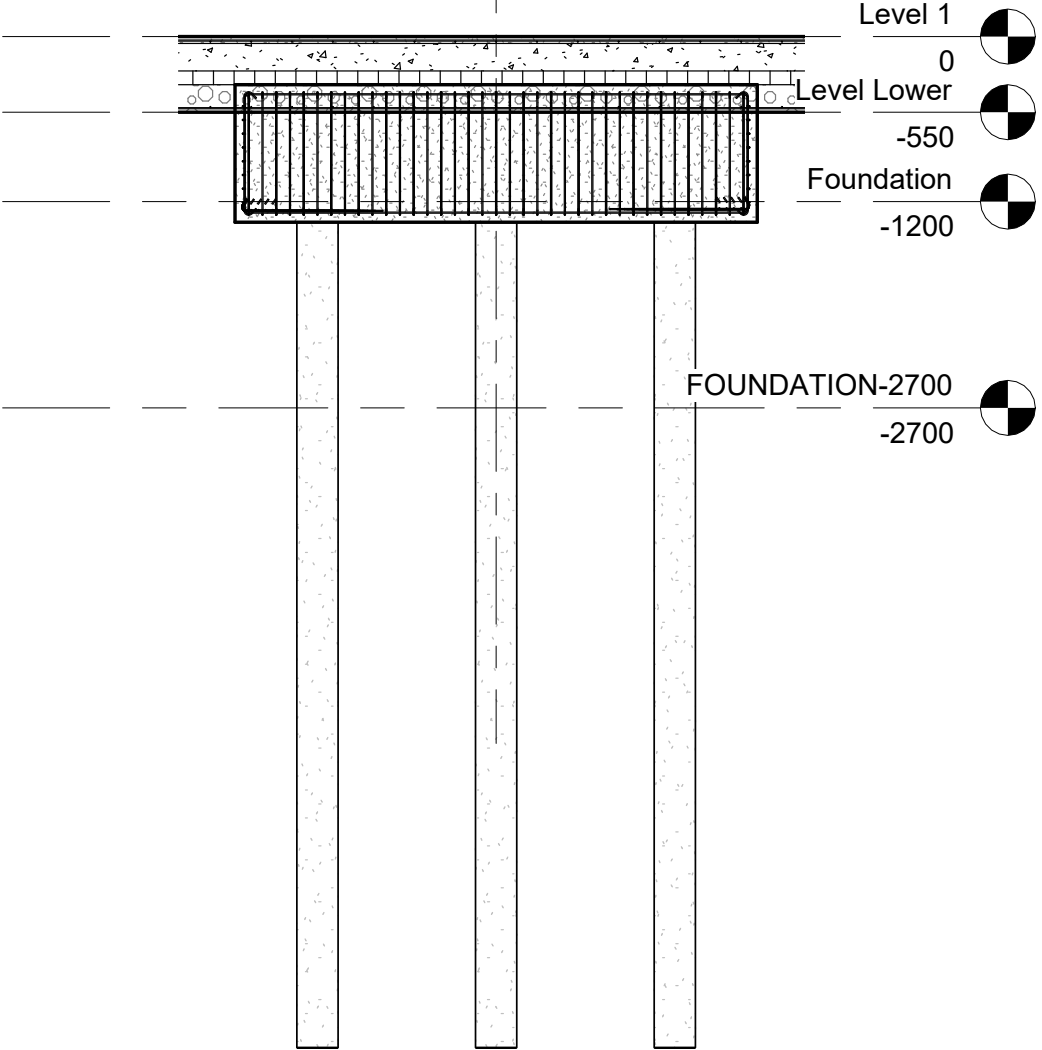

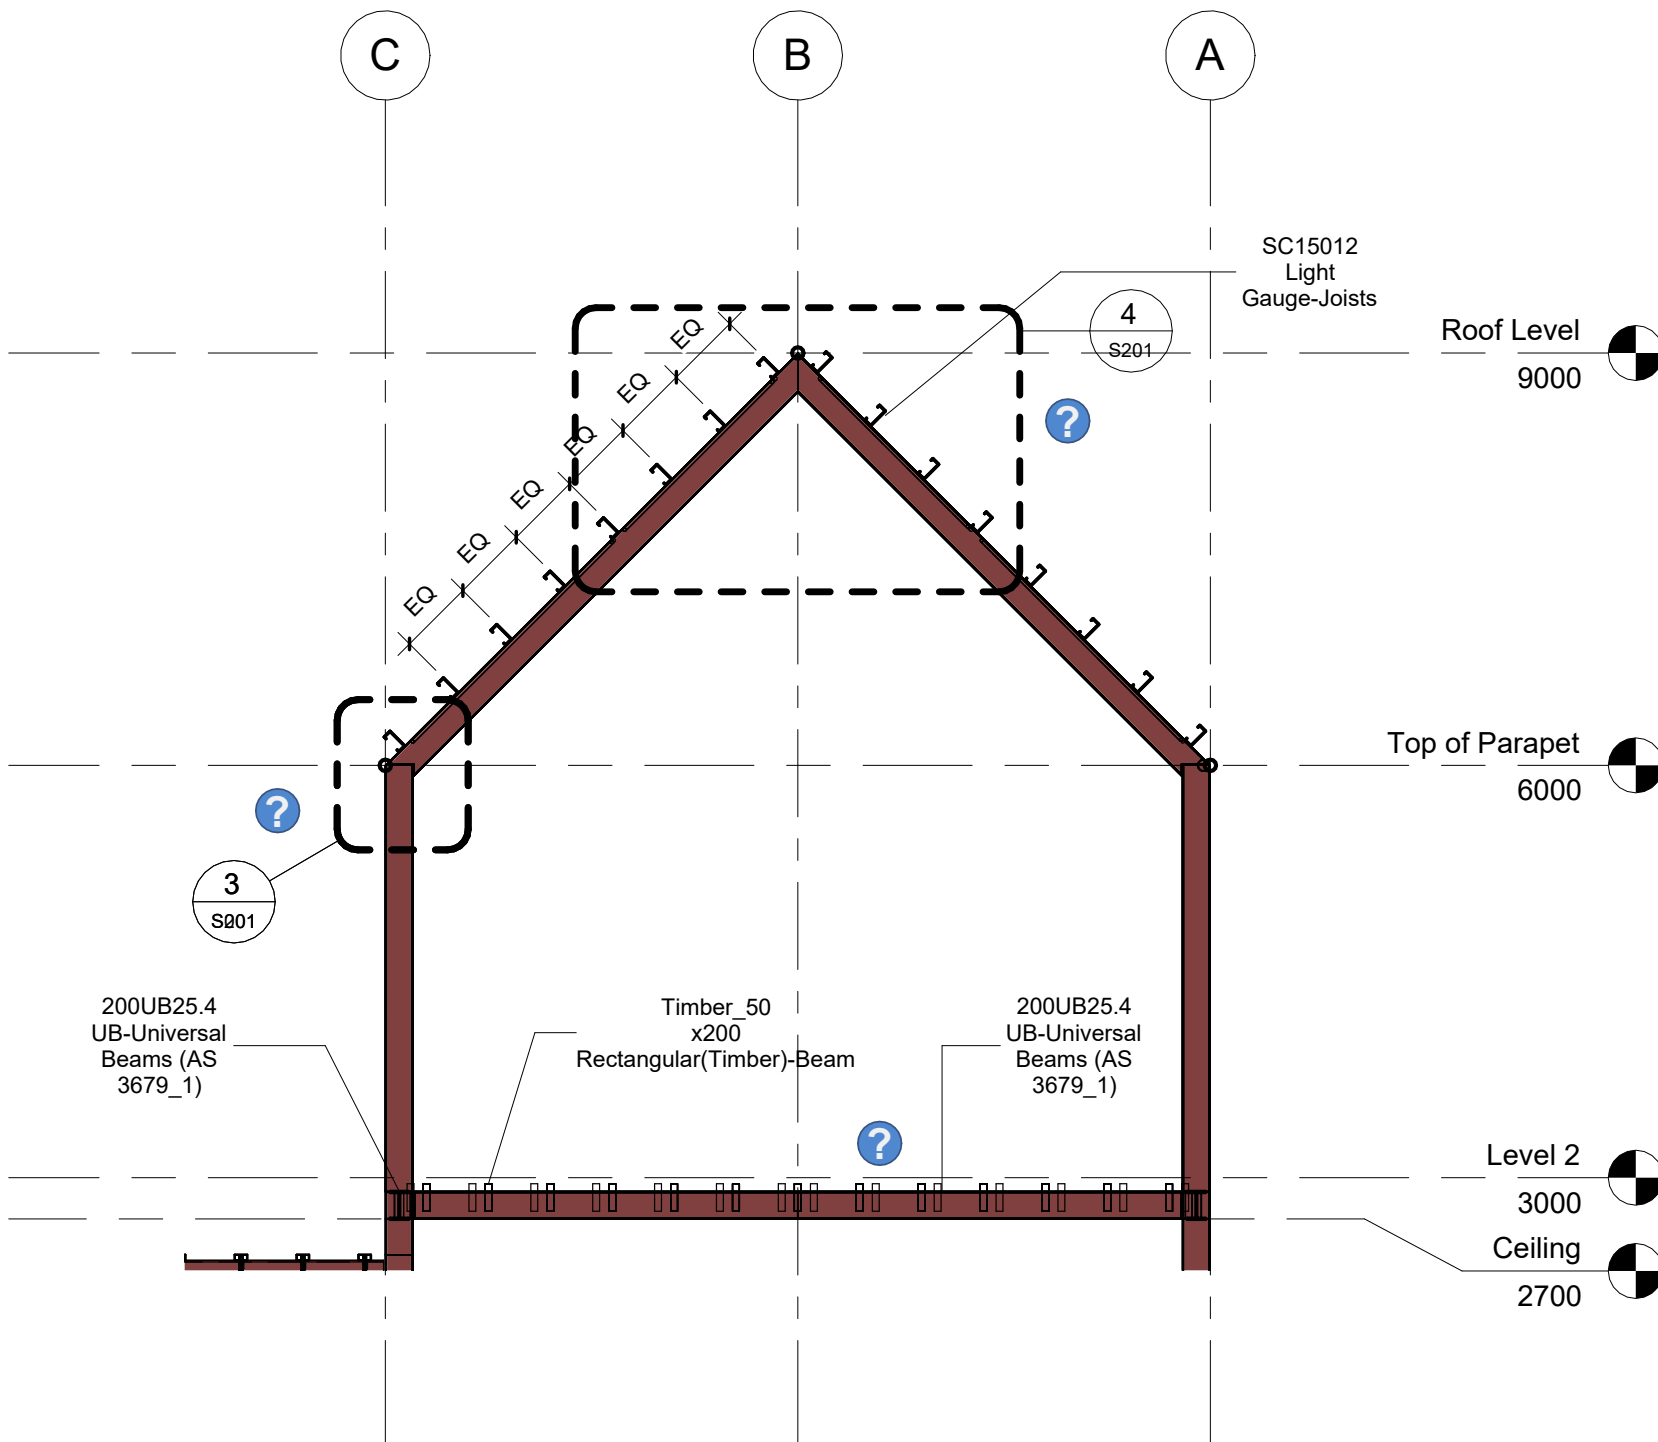

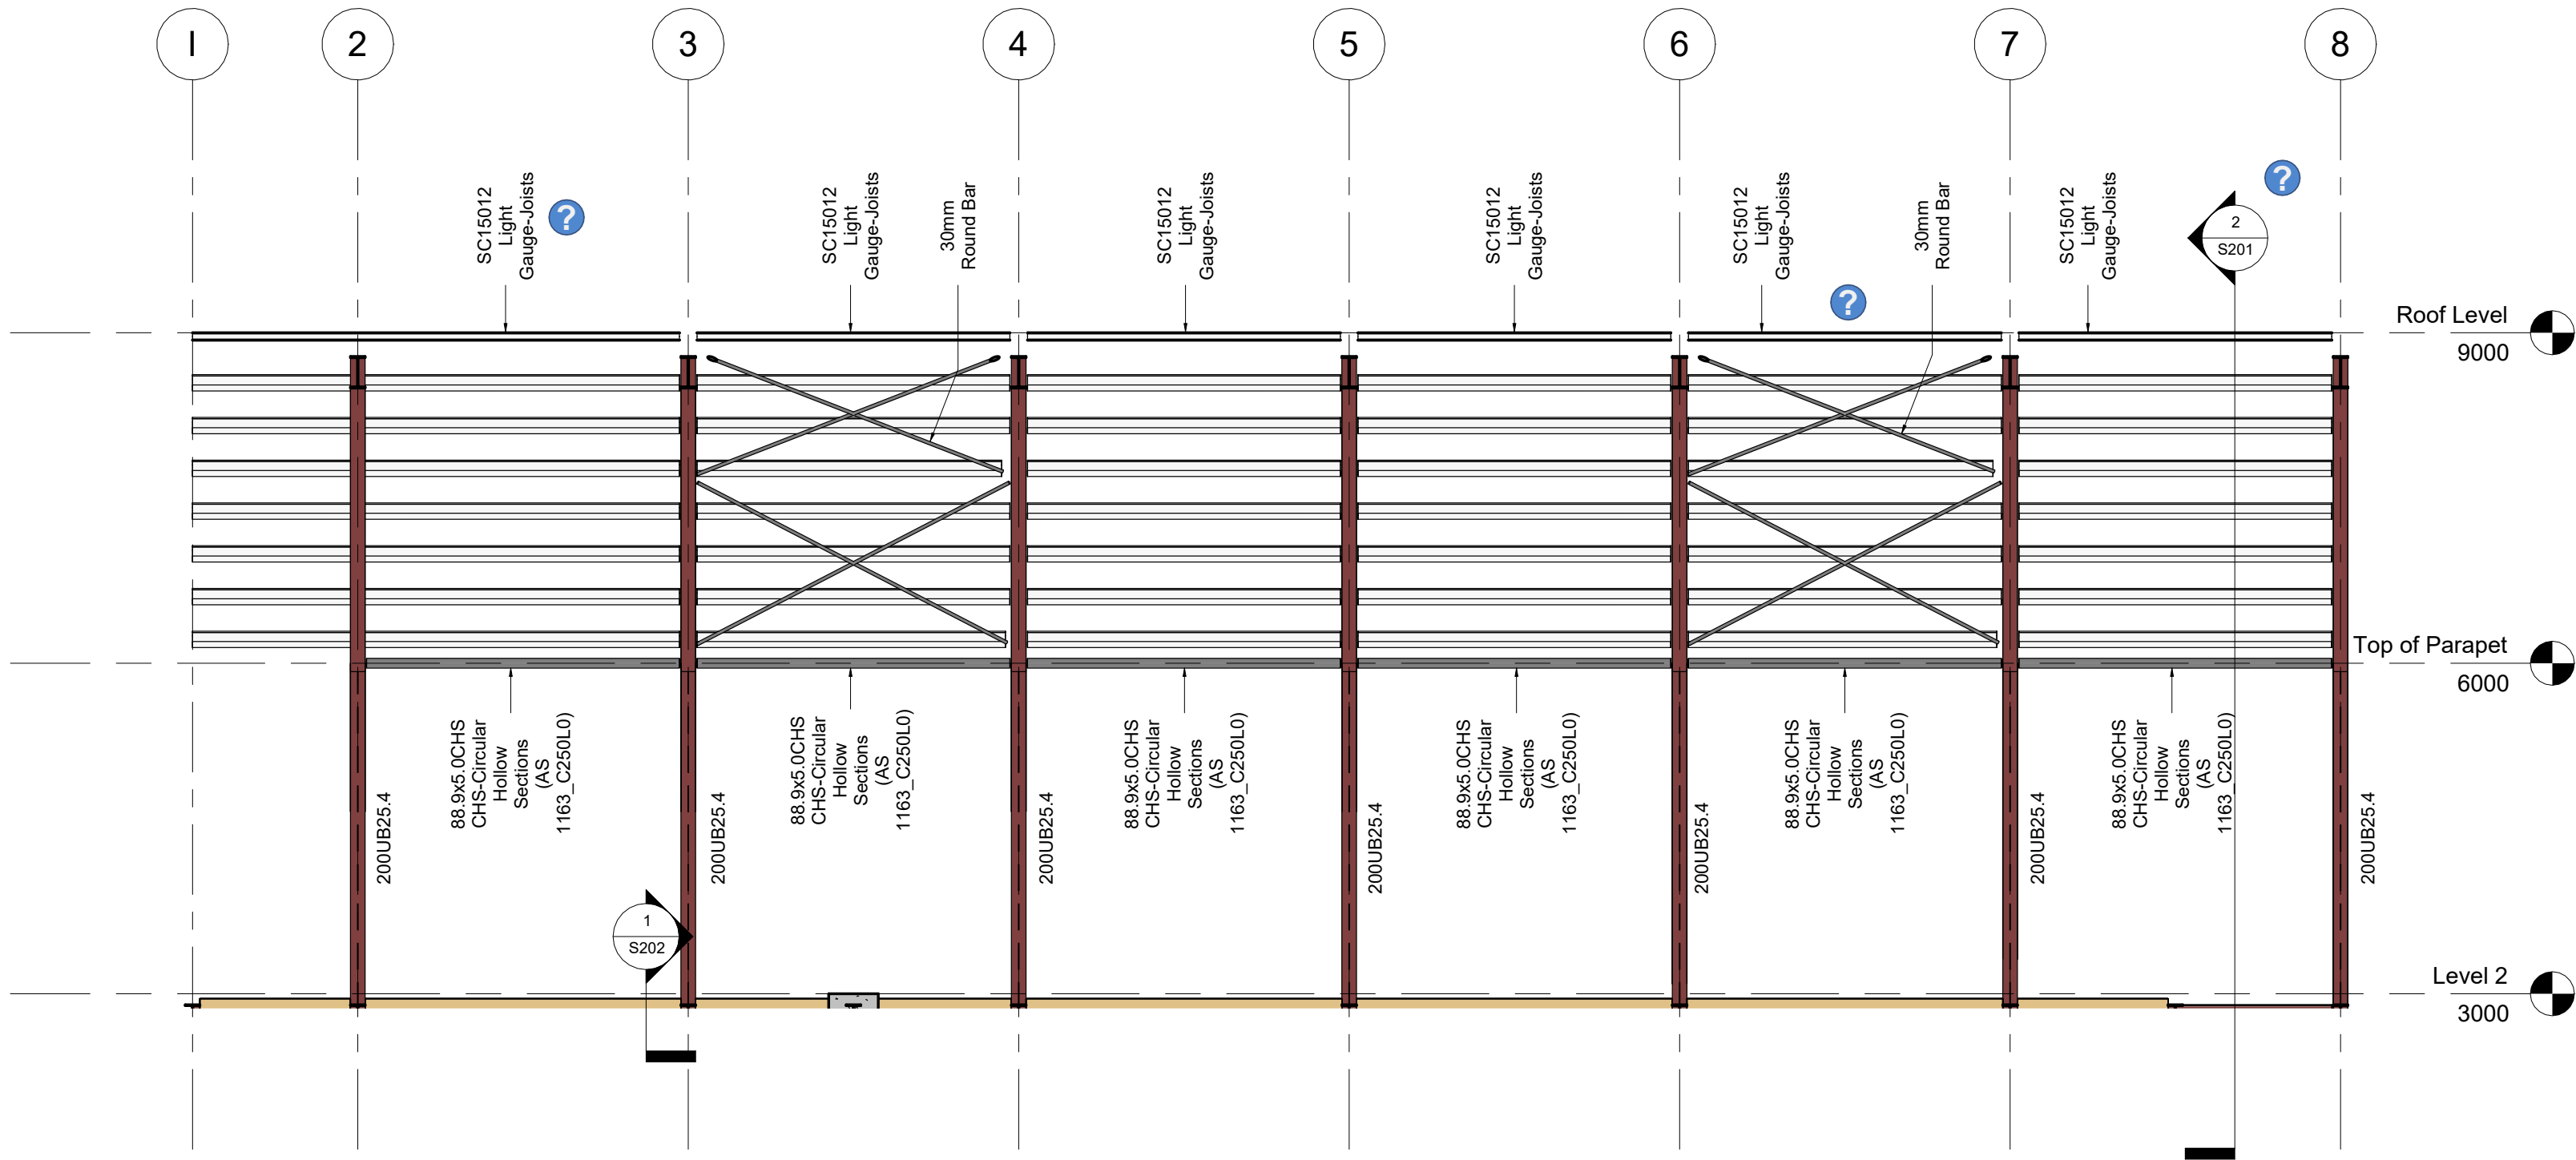

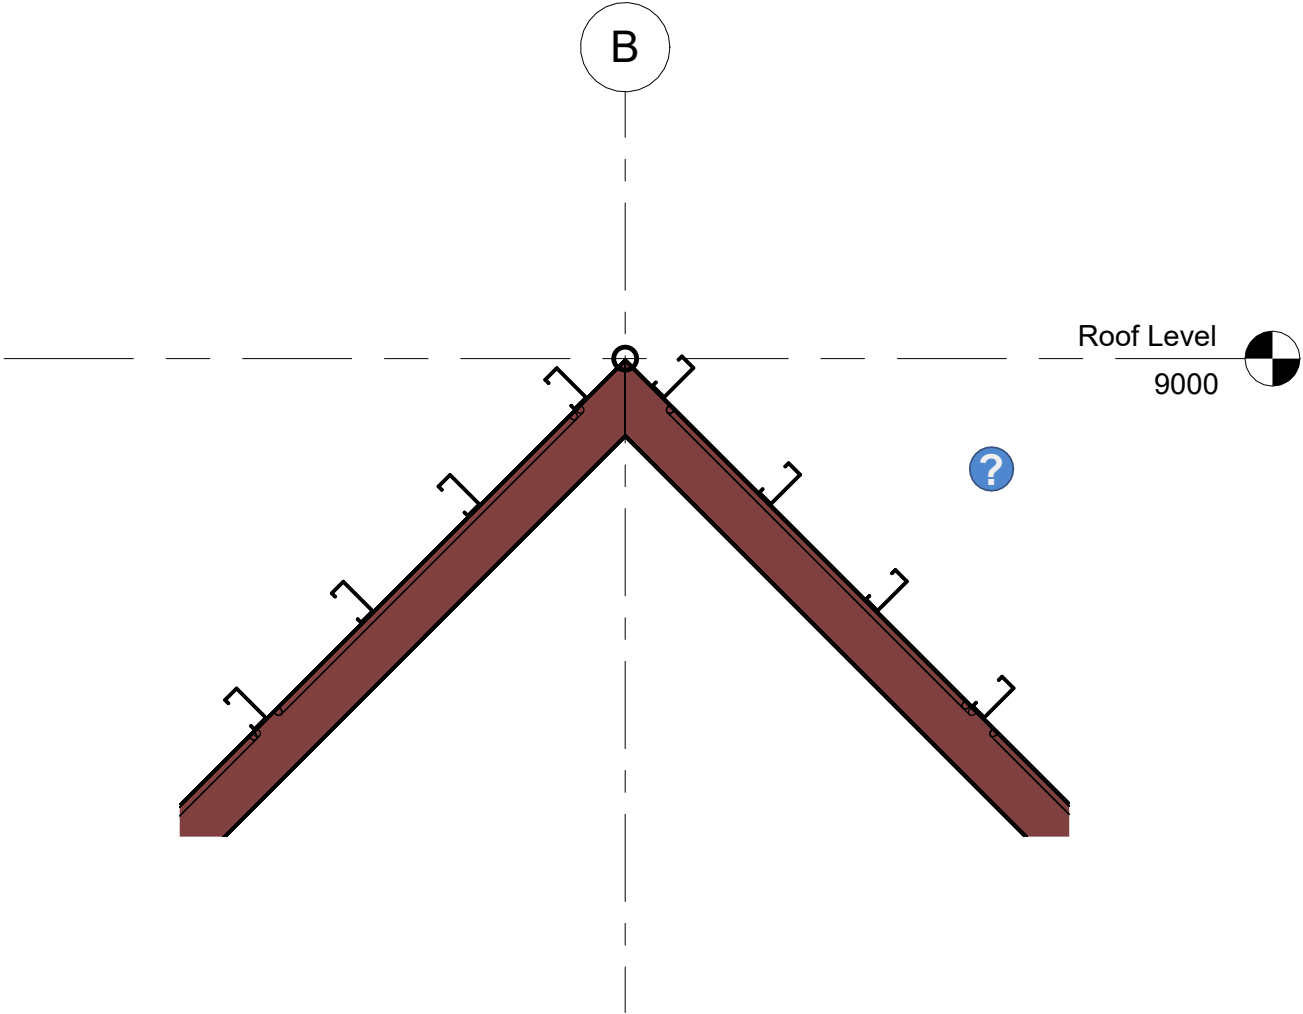

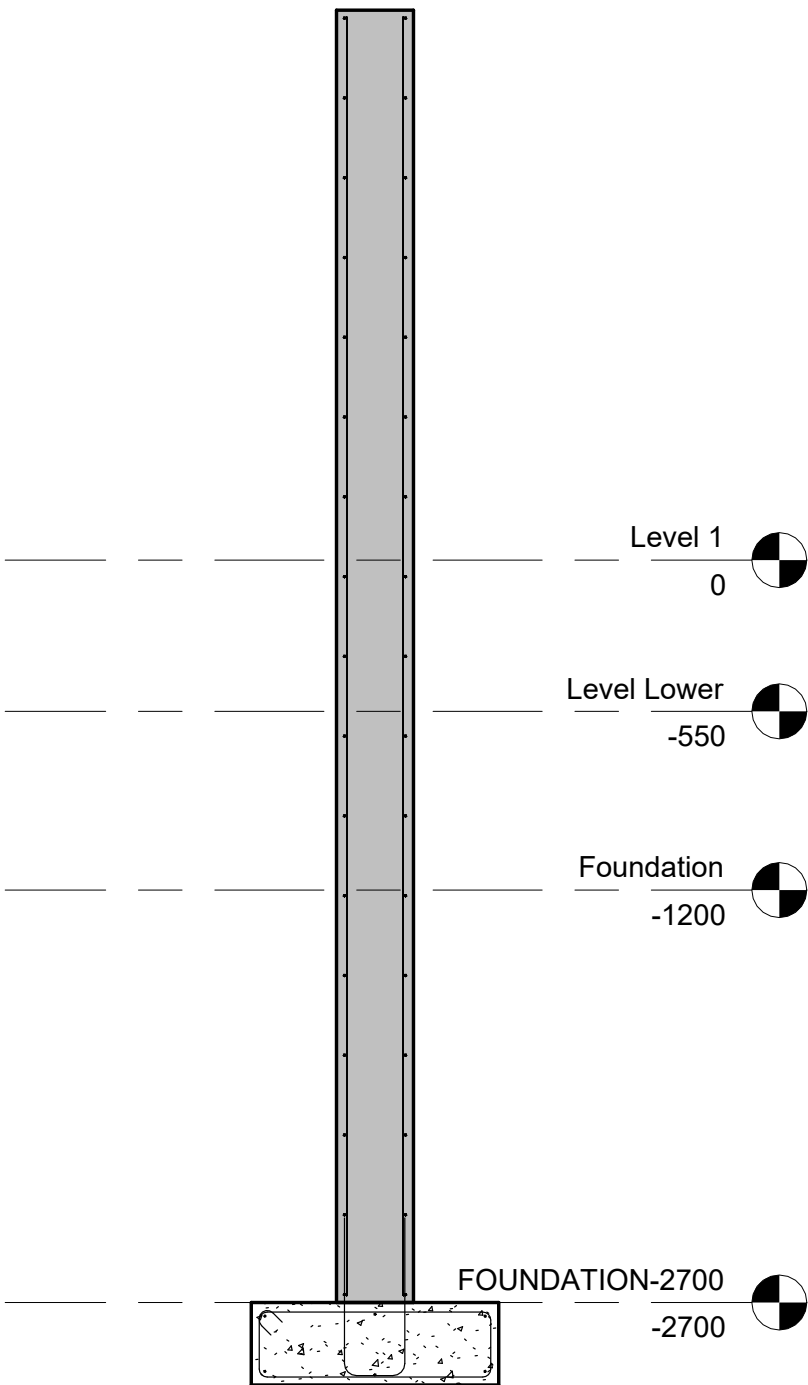

C

SC15012
Light
Gauge-Joists

88.9x5.0CHS
CHS-Circular
Hollow
Sections
(AS
1163_C250L0)

Top of Parapet
6000

200UB25.4
UB-Universal
Beams (AS
3679_1)

200UB25.4

